南京西路—仁愛路沿線｜紅框範圍：都市計畫個案與更新意圖

底圖：A01_A10_Nanjing_Renai_20261005 第 1 頁線稿（1:10000，已移除 A01–A10 框線與框內建物填色）。紅框＝沿線 24 個都市計畫個案範圍（民國 90 年後公告、與原十幅相交者及臺北車站特專區），編號由西向東；斜線＝劃定更新地區。下方依分段總結更新意圖。

都市計畫個案範圍　劃定更新地區（P089016、P097017、獎勵更新地區等）　行政區通檢範圍界

格網北

0　500　1000 m

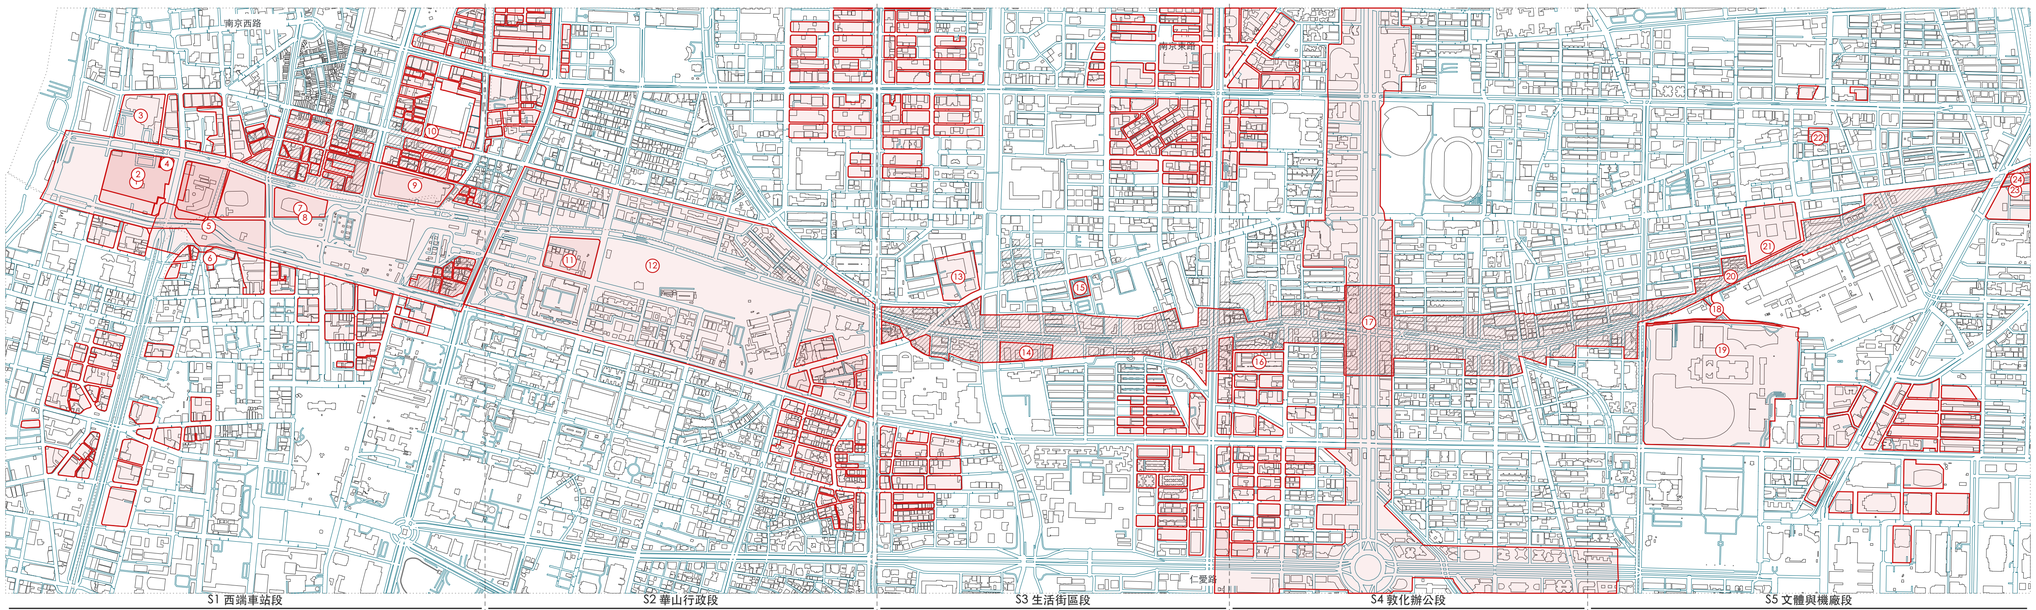

S1 西端車站段　環河北路—中山北路

S2 華山行政段　中山北路—新生北路

S3 生活街區段　新生北路—復興南路

S4 敦化辦公段　復興南路—光復南路

S5 文體與機廠段　光復南路—基隆路

各段更新意圖

S1 西端車站段

環河北路—中山北路｜大同、中正

以特定專用區與聯合開發，把鐵路地下化釋出的公有地轉為交通、辦公與博物館複合核心；同時以古蹟活化（北門、鐵道工場、當代館、郵電大樓）重建歷史地景，並要求臨路帶狀開放空間緩衝高架。

S2 華山行政段

中山北路—新生北路｜中正、中山

以整體規劃、整體開發重組華山：南側強化中央行政主體並保留文創大街廊，北側六條通升格商業但不增強度；行二行三以公辦都更兼顧原住戶安置，並禁止容積移入以維持環境品質。

S3 生活街區段

新生北路—復興南路｜中山、大安

不增容積、只放寬使用組別並劃定更新地區，鼓勵老舊住宅自主改建；以開放空間、人行通道換取獎勵，搭配 TOD 於站點周邊適度加密，逐步形塑市民大道東西向景觀軸與人行空間。

S4 敦化辦公段

復興南路—光復南路｜松山、大安

維持敦化南北路辦公金融特性，沿市民大道以住四之一（特）放寬支援性商業；更新以既有大型基地為主，TOD 引導忠孝復興站周邊加密。

S5 文體與機廠段

光復南路—基隆路｜信義、松山

將菸廠、唐榮等工業遺址轉為文化體育與大型商業設施，並以新闢道路補強路網；八德路以北以老舊中低層社區專案與公辦都更推動小街廓更新，松山車站整合為東區轉運門戶。

紅框一覽｜依所在分段排列（計畫書全文與願景摘要見整合文字檔）

S1 西端車站段

1. P108001　E1／E2／D1 細部：博物館特專區，臨路 10 m 帶狀開放空間
2. P107017　E1／E2／D1 主要：公設用地轉特專區、博物館特專區
3. P115011　中興醫院：建蔽放寬，地下連通北門站
4. P093040　北門站：捷運出入口＋劃定更新地區
5. P105006　北門廣場：拆引道，重現北門城地景
6. P096016／P096022　郵電大樓：古蹟保存，交大使用
7. P095016／P095018　C1／D1 聯開（雙子星）：機捷站與聯合開發
8. P082022／P082023　臺北車站特專區：交通運輸中心框架
9. P093053　交九：轉運站立體共構
10. P091007　當代館：舊市府古蹟活化

S2 華山行政段

11. P111010　行二行三：行政主體、附屬使用 ≤30%
12. P092029／P092034　華山整體計畫：行政／文創專用區、六條通商三（特）

S3 生活街區段

13. P114001　工業區轉大學用地（待核）
14. P093013／P098027　懷生段：開放空間換容積（臺北好好看）
15. P092003-07／P093011-07　中油加油站：轉作住商或公園

S4 敦化辦公段

16. P108006　TOD：站點周邊開發許可加密
17. P091017　敦化特專區：辦公金融單一分區

S5 文體與機廠段

18. P099046　松菸北側：工業區改道路
19. P092031／P092044　松菸特專區：大巨蛋＋古蹟再利用
20. P097017　市民大道兩側：放寬使用組別＋更新地區
21. P103018／P107003　唐榮／京華城：商三（特）多目標、分 2 區
22. P109004　西松段：老舊社區專案更新
23. P093038　松山車站：東區轉運樞紐
24. P090031　南港專案：鐵路地下化東延

資料：臺北市都發局歷年計畫索引與計畫書（查詢 2026-10-05）；案件階段沿用《簡要標記 v2》《公共都更與公共建設編號圖》（查核 2026-10-04）；地號：臺北市地籍 GIS；現況建物：OSM。分段特性為規劃觀察，非法定判定。底圖 © OpenStreetMap contributors / ODbL｜100% 列印勿縮放