N

1:8,000

0 100 200 500 1,000 m

市民大道沿線｜歷史圖資痕跡疊圖

200 m 方格中，現況街廓佔 30% 以上者置入當年地圖（反黑），其餘為現況圖底（諾利圖）；淡水河堤外不置入。

1904

日治臺灣堡圖（明治版）

原圖 1:20,000

可見痕跡

水圳、埤塘（上埤頭）、鐵道

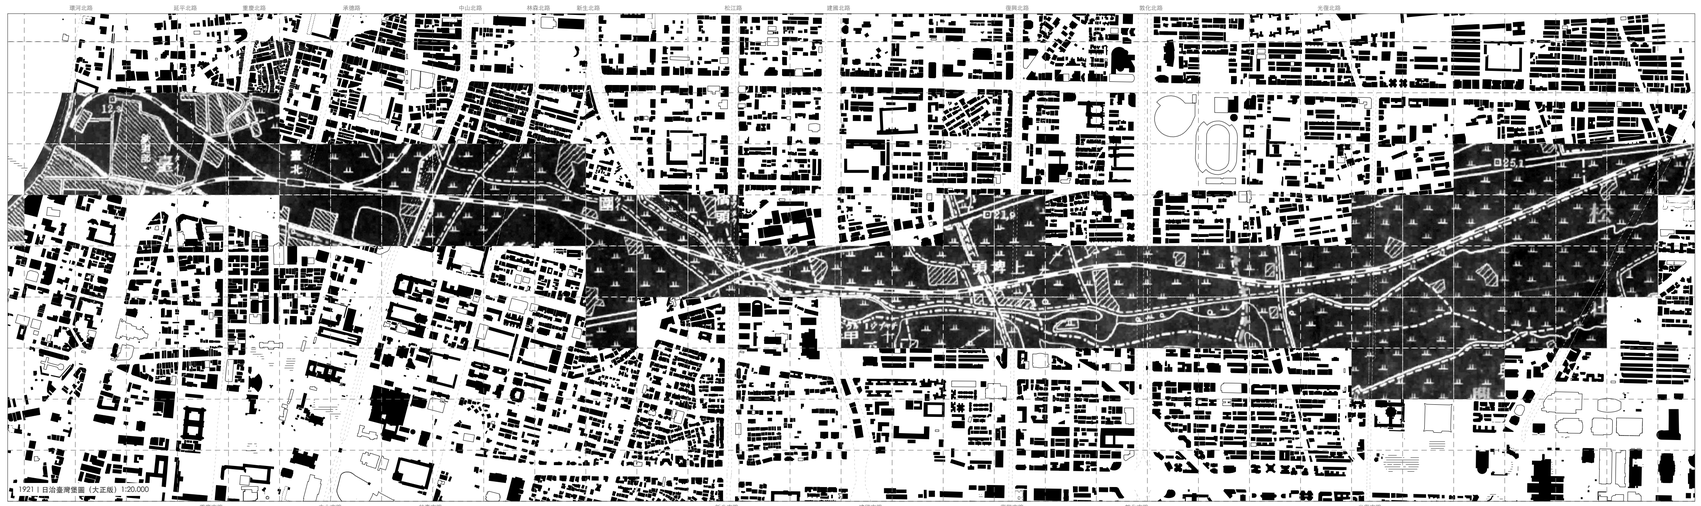

1921

日治臺灣堡圖（大正版）

原圖 1:20,000

可見痕跡

水圳、埤塘、鐵道——與 1904 對照

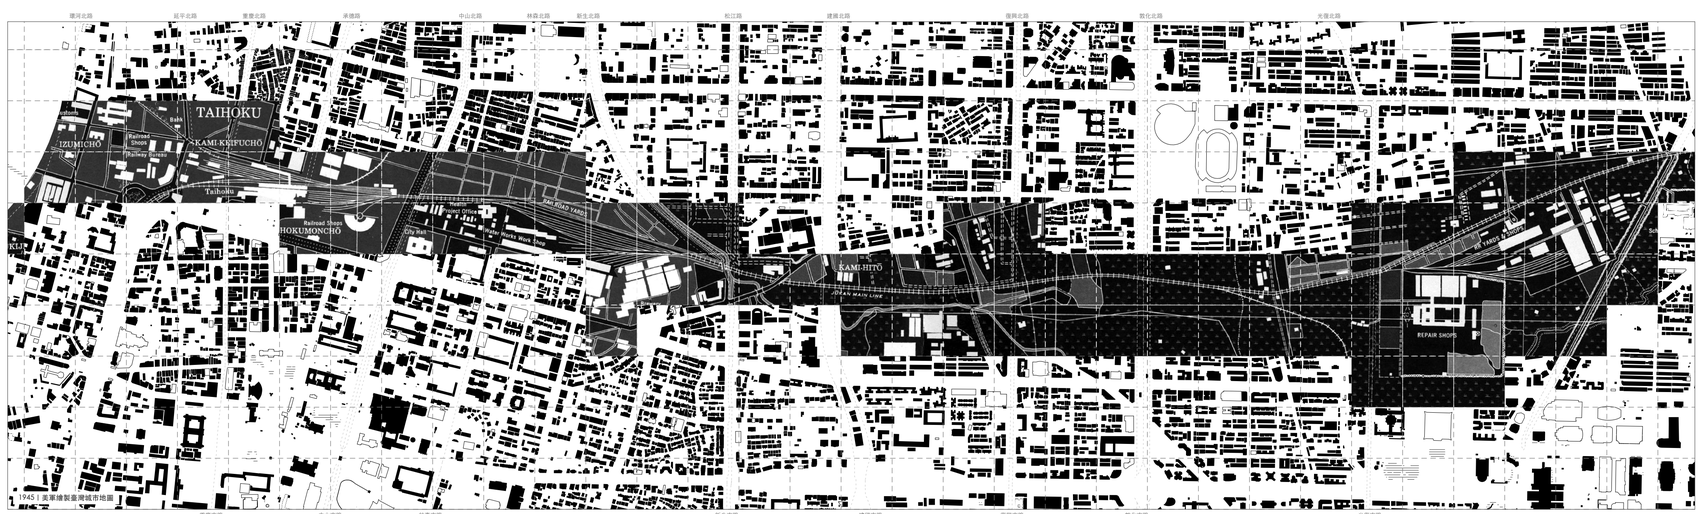

1945

美軍繪製臺灣城市地圖

可見痕跡

縱貫線、調車場、鐵道部、機廠、酒廠

當年地圖（反黑）

現況圖底（諾利圖）

200 m 方格

1:12,000（A1）

0 250 500 1000 m

N

資料：中央研究院人社中心 臺灣百年歷史地圖（JM20K_1904、JM20K_1921、AMCityPlan_1945）；現況圖底 © OpenStreetMap contributors

計畫範圍與都市發展、都更案例

建物依所屬行政區（通盤檢討細部計畫範圍）著色，紅→藍由西向東；區界內縮拉開、不繪道路，留白即街道。黑線＝市民大道。都更與發展案例以單一深色剪影、基地範圍及編號標示，編號由西向東，案件狀態見下方說明。

格網北

計畫範圍　大同區 P110002　萬華區 P110001　中正區 P111021　中山區 P110025　大安區 P110013　松山區 P108012　信義區 P112014　市民大道　案例　建物剪影　敷地／裙樓　基地範圍　基地概括／推估（虛線）　1 案件編號　結案未續行

1:8,699　0　500　1000 m

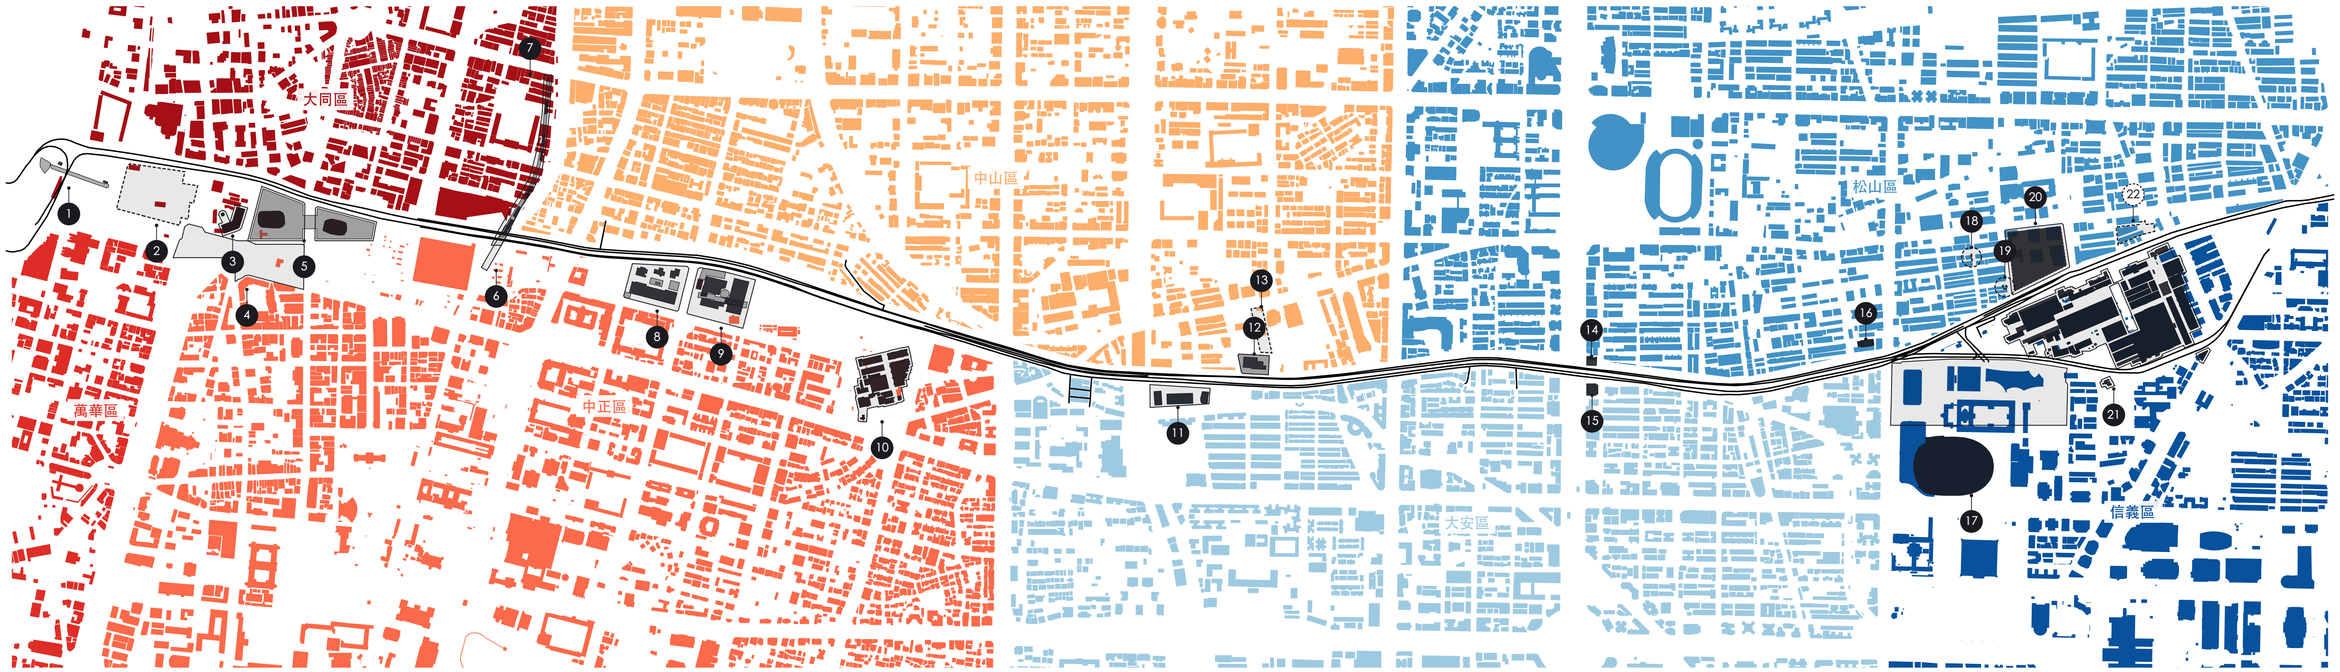

S1 西端車站段	S2 華山行政段	S3 生活街區段	S4 敦化辦公段	S5 文體與機廠段
環河北路—中山北路	中山北路—新生北路	新生北路—復興南路	復興南路—光復南路	光復南路—基隆路

各段更新意圖

S1 西端車站段

環河北路—中山北路｜大同、中正

鐵路地下化釋出土地轉為交通、辦公、博物館核心；古蹟活化重建歷史地景。

S2 華山行政段

中山北路—新生北路｜中正、中山

南側強化中央行政、保留文創街廓；北側六條通升格商業；行二行三公辦都更。

S3 生活街區段

新生北路—復興南路｜中山、大安

不增容積、放寬使用並劃定更新地區；以開放空間換獎勵，形塑東西向景觀軸。

S4 敦化辦公段

復興南路—光復南路｜松山、大安

維持辦公金融特性；沿市民大道放寬支援性商業，TOD 引導站點周邊加密。

S5 文體與機廠段

光復南路—基隆路｜信義、松山

工業遺址轉文化體育與商業；老舊社區公辦都更；松山車站為東區轉運門戶。

案件狀態說明｜依所在分段排列

推動階段：規劃中 → 前期／招商 → 審議中 → 審議通過 → 施工中／展延 → 已完成；另列 結案未續行。★＝推定待核

1 玉泉公園人本跨橋　［規劃中］

公共工程｜水利處｜堤內外人行與自行車跨橋，含電梯、階梯與牽引道；把西端車站區接回淡水河水岸，尚非定案構線。

2 臺北車站 E1／E2　［審議中］

公有地都更｜鐵道局｜鐵道局公有地都更，更新單元 17 筆約 1.6 ha，位於北門與車站西側；2023 報核、2024 公展，考古試掘與文資修復同步進行。未來為博物館特專區＋商業，臨鄭州路留 10 m 帶狀開放空間。

3 鐵道部園區（鐵道博物館）　［已完成］

文資｜臺博館｜臺灣總督府交通局鐵道部古蹟修復為鐵道歷史博物館（2020 開館）。

4 北門廣場　［已完成］

公共空間｜市府｜忠孝橋引道拆除後重現北門城與城牆地景（2017）；與鐵道部、三井倉庫串成北門文資節點。

5 臺北雙子星（C1／D1）★　［施工中／展延］

聯合開發｜機捷｜機捷臺北站上方聯開，C1 55F 辦公商城、D1 74F 企業總部＋旅館＋觀景台，裙樓設國門客廳並跨重慶北路相連；預計 116 年完工。塔樓剪影取自 OSM 興建中輪廓（D1 約 3,340 ㎡、C1 約 2,480 ㎡）；跨重慶北路之連續裙樓依展覽模型推估。

6 跨市民大道空廊（Skywalk）★　［前期／招商］

公共工程｜臺北捷運公司｜城市大道計畫之跨市民大道段（發包中）：連續空廊、大尺度行人穿越道與頂棚，自心中山南端跨越市民大道接臺北車站，模型顯示步行平台穿越高架橋下。位置依心中山軸線南延推估。

7 心中山線形公園　［已完成］

公共空間｜北捷｜城市大道（Skywalk）計畫之公園段，2025-08 完工；捷運淡水線上方線形公園，南端 R1 出入口緊鄰市民大道。

8 台灣心 HUB（行二行三）　［審議通過］

公辦｜住都中心／冠德｜住都中心公辦、冠德出資，基地 18,365 ㎡；辦公棟 22F（88.6 m）、住宅棟 24F（89.6 m），預計 2031 完工。現住戶原地安置；「台北心軸線」New Civic Hub 核心，與南側司法園區隔市民大道相對。

9 華山司法園區　［施工中／展延］

公共建設｜司法院｜華山行六用地司法機關遷建；2022 先期工程動土，期程展延。完工後南側新增大量公務人流。

10 華山 1914 文創園區　［已完成］

文資｜文化部｜創意文化專用區內之酒廠古蹟群，假日文創人流核心。

11 明日博／懷生段931　［已完成］

私人｜「臺北好好看」｜「臺北好好看」專案，市民大道三段×建國南路，東西兩基地約 0.9 ha，2016 完成；以廣場式開放空間、地面人行通道換取容積獎勵，是沿線少數已兌現的地面開放空間樣本。

12 長安市民公辦都更　［審議中］

公辦｜住都中心／潤泰｜住都中心公辦、潤泰創新實施，5 筆約 0.45 ha；2025-11 公展、12 月公辦公聽會，審議中。23 層住宅，1F 托嬰中心＋店鋪，臨市民大道退縮約 17 m 開放空間（建蔽約 35%）。

13 中油中山公辦都更　［前期／招商］

公辦｜前期｜原中油加油站用地（P092003／P093011 變更），4 筆約 0.41 ha；2026-05 選定公辦都更，招商準備中、尚無配置。位於市民大道與八德路之間，可能改變南北穿越路徑。

14 德杰（敦化×市民 東北）★　［已完成］

私人｜德杰案，延吉段三小段 831-1 等，敦化×市民東北角；已完成並成果備查。剪影以東北角 22F 敦南樓苑推定，待核。

15 富邦（敦化×市民 東南）　［已完成］

私人｜富邦案，仁愛段六小段 245-2 等，敦化×市民東南角；已完成（富邦敦南大樓）。與 U05 分屬道路兩側，可比較不同退縮與商業介面。

16 麗寶（光復×市民 西北）　［已完成］

私人｜麗寶案，延吉段一小段 175 等，光復×市民西北角；已完成並成果備查，代表光復節點既有更新成果。

17 臺北大巨蛋／松菸　［已完成］

BOT｜市府｜松菸特專區之大巨蛋（2023 啟用）與松山文創園區；平日中等、活動散場為極端尖峰。

18 青園（光復 13、17 巷）　［審議中］

私人｜申請審查｜青園案，西松段三小段 281 等 18 筆，光復南路 13、17 巷；2026 申請審查、尚未核定。後續看更新範圍與巷道通行設計。

19 旭豐（八德 72、106 巷）　［審議中］

私人｜申請審查｜旭豐案，西松段三小段 454 等 43 筆，八德路 72、106 巷；2026-06 申請審查，舊事業概要與本次申請需分開辨識。

20 京華城重建 ★　［施工中／展延］

私人｜威京｜原唐榮鐵工廠商三（特）基地重建為大型商業辦公；土地扣押中、變更設計待審，無公開配置。量體以基地內縮 8 m 示意（虛線）。

21 臺北機廠（國家鐵道博物館）★　［施工中／展延］

文資｜文化部｜國定古蹟臺北機廠轉為國家鐵道博物館園區，分期修復開放；與大巨蛋形成南北軸。

22 機廠北側 7599　［結案未續行］

公辦｜已停止｜公辦案，西松段三小段 58 等 33 筆約 0.39 ha，臺北機廠北側；2025-10 因所有權人意願未達門檻結案。保留對照，顯示小街廓整合困難。

資料：臺北市都發局歷年計畫索引與各區通盤檢討（查詢 2026-10-05）；案件階段沿用《簡要標記 v2》《公共都更與公共建設編號圖》並補展覽資料（2026-10-04）；建物：統一清理 v2 擴幅建物輪廓；表現法參考 Architecture Workroom Brussels, Thinkers versus Makers (2016)。底圖 © OpenStreetMap contributors / ODbL

都市計畫個案 × 公告當年航照

紅框內為該案公告當年之臺北市正射影像（黑白）；當年無影像者取最近一年。

都市計畫個案範圍　　行政區通檢範圍界　　幹道

格網北

0　500　1000 m

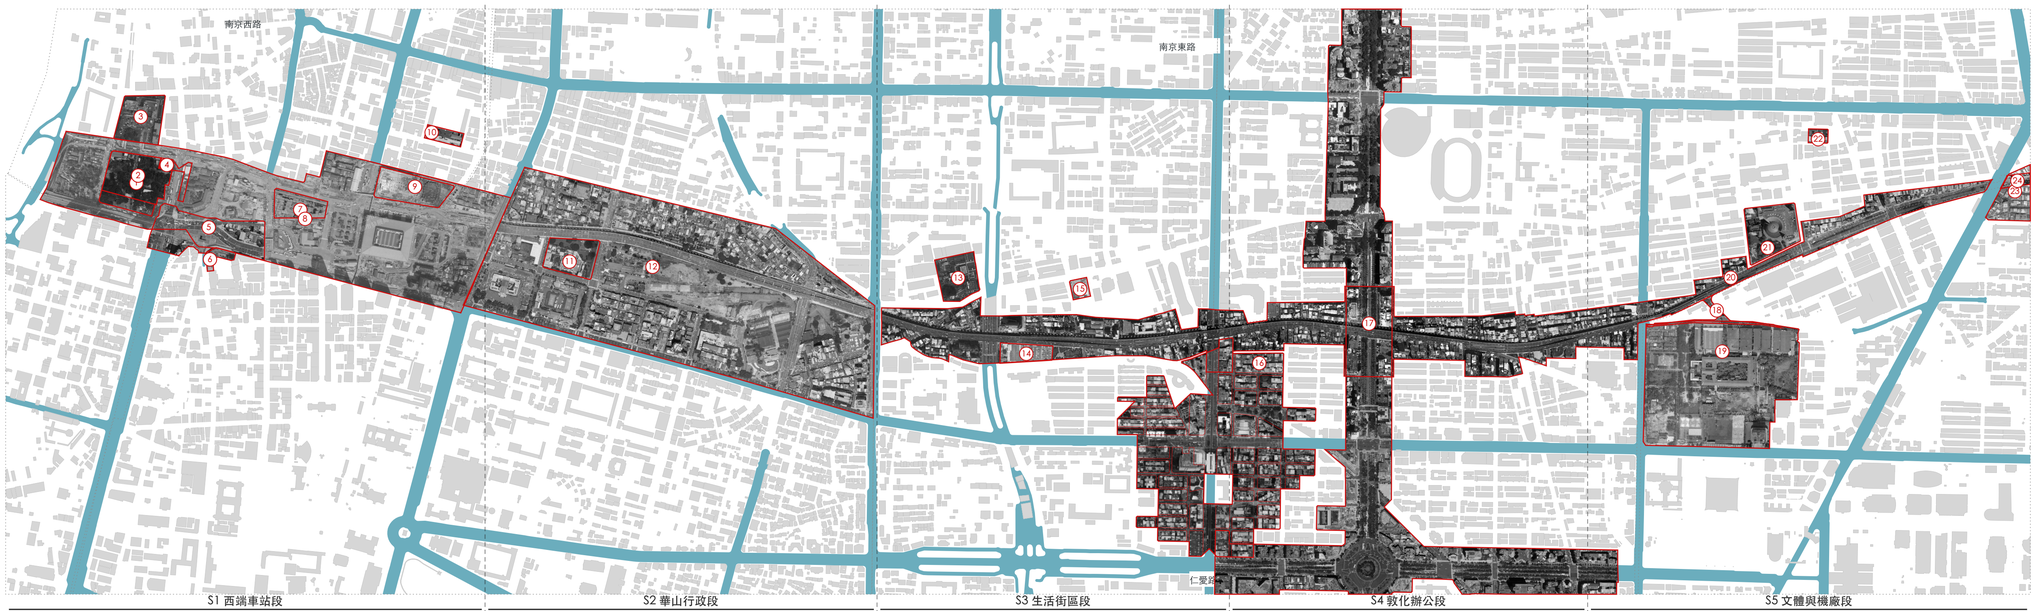

S1 西端車站段
環河北路—中山北路

S2 華山行政段
中山北路—新生北路

S3 生活街區段
新生北路—復興南路

S4 敦化辦公段
復興南路—光復南路

S5 文體與機廠段
光復南路—基隆路

各段更新意圖

S1 西端車站段
環河北路—中山北路｜大同、中正

鐵路地下化釋出土地轉為交通、辦公、博物館核心；古蹟活化重建歷史地景。

S2 華山行政段
中山北路—新生北路｜中正、中山

南側強化中央行政、保留文創街廊；北側六條通升格商業；行二行三公辦都更。

S3 生活街區段
新生北路—復興南路｜中山、大安

不增容積、放寬使用並劃定更新地區；以開放空間換獎勵，形塑東西向景觀軸。

S4 敦化辦公段
復興南路—光復南路｜松山、大安

維持辦公金融特性；沿市民大道放寬支援性商業，TOD引導站點周邊加密。

S5 文體與機廠段
光復南路—基隆路｜信義、松山

工業遺址轉文化體育與商業；老舊社區公辦都更；松山車站為東區轉運門戶。

紅框一覽

①	2019	E1／E2 細部｜博物館特專區
②	2018	E1／E2 主要｜公設用地轉特專區
③	2026	中興醫院｜地下連通北門站（影像 2025）
④	2004	北門站｜捷運出入口
⑤	2016	北門廣場｜拆引道
⑥	2007	郵電大樓｜古蹟保存
⑦	2006	C1／D1 雙子星｜聯合開發
⑧	1993	臺北車站特專區｜交通運輸中心
⑨	2004	交九｜轉運站
⑩	2002	當代館｜舊市府活化
⑪	2022	行二行三｜中央行政主體
⑫	2003	華山整體計畫｜行政／文創專用區
⑬	2025	工業區轉大學用地
⑭	2004	懷生段｜開放空間換容積
⑮	2003	中油加油站｜轉作住商或公園
⑯	2019	TOD｜站點周邊加密
⑰	2002	敦化特專區｜辦公金融
⑱	2010	松菸北側｜工業區改道路
⑲	2003	松菸特專區｜大巨蛋
⑳	2008	市民大道兩側｜放寬使用
㉑	2014	唐榮／京華城｜商業多目標
㉒	2020	西松段｜老舊社區更新
㉓	2004	松山車站｜東區轉運樞紐
㉔	2001	南港專案｜鐵路地下化東延

影像：臺北市歷史圖資展示系統（1994–2025）｜計畫：臺北市都發局都市計畫書｜底圖 © OpenStreetMap contributors

市民高架沿線｜一樓使用現況

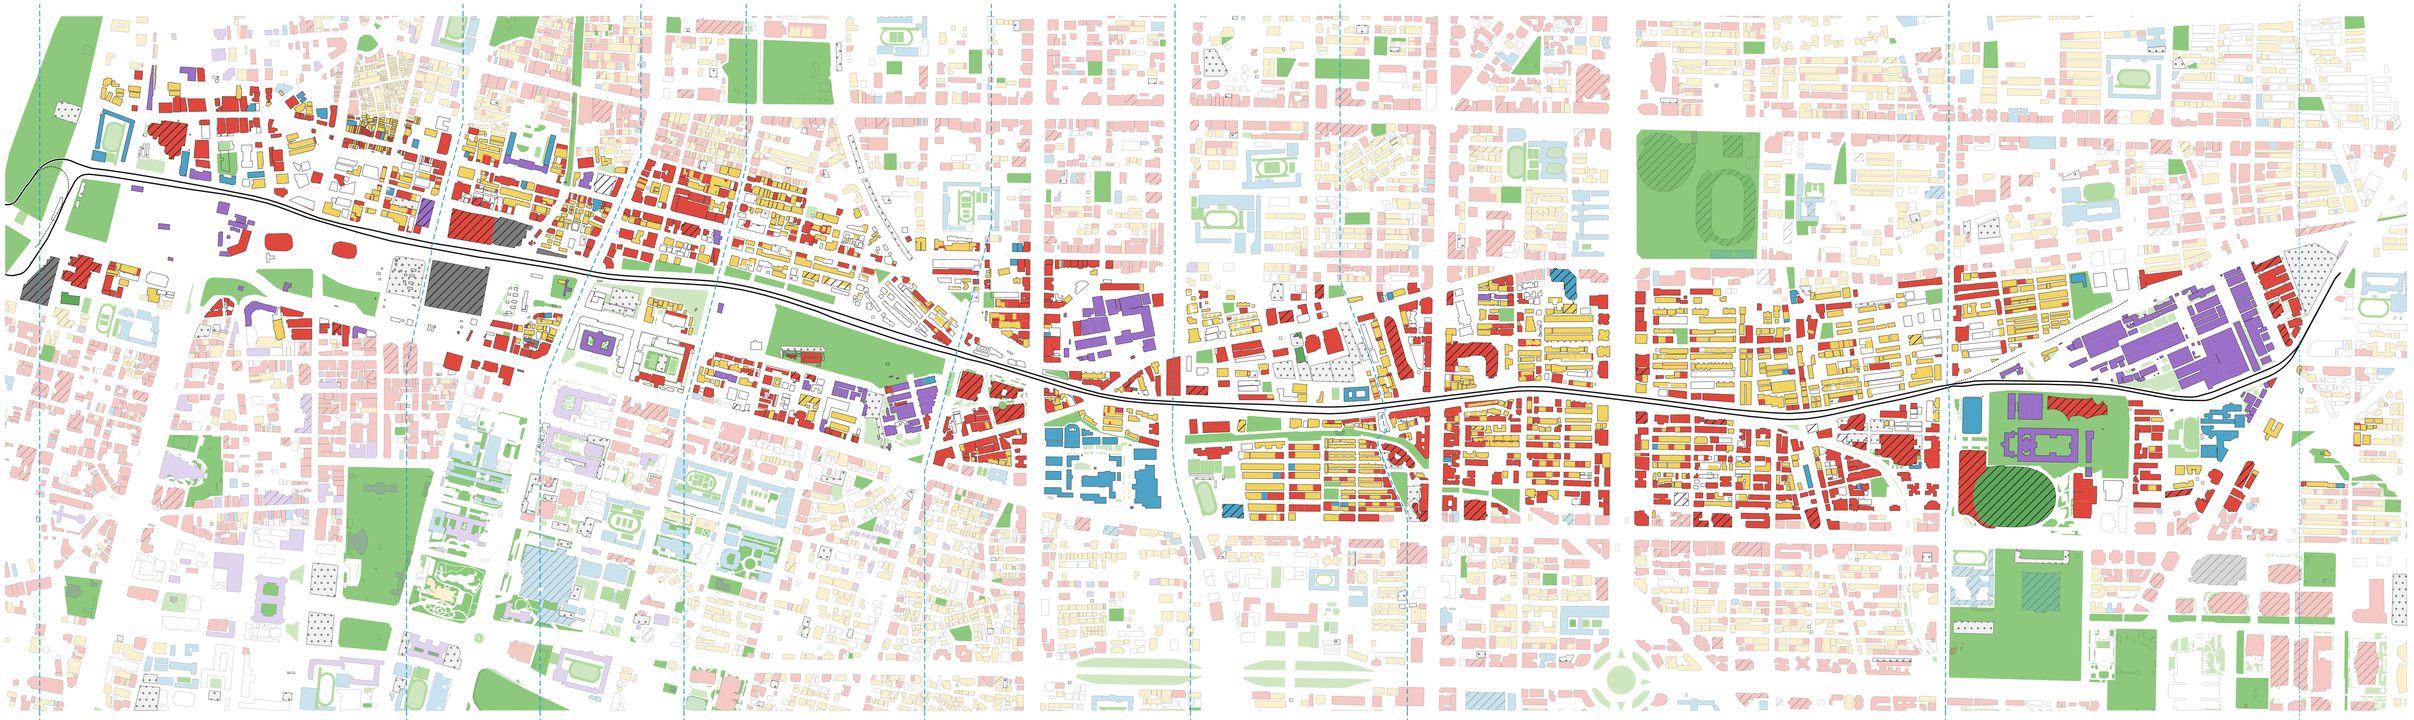

住宅
商業
產業與古蹟
停車與交通
醫療／文教
運動休閒
公園
草地／樹林
運動場／遊戲場
平面停車場
含停車場之建物
市民高架
匝道
設計介入單元 Z1 - Z8
高架兩側 300 m 範圍
範圍外

0 250 500 1000 m

各用途於 Z1 - Z8 的變化

住宅　12 - 47%

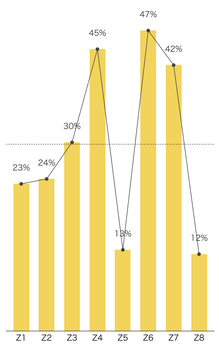

商業　29 - 61%

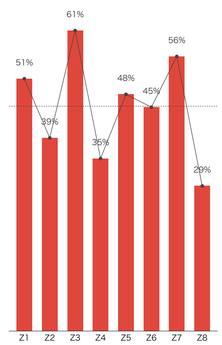

產業　0 - 38%

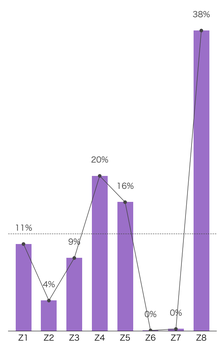

停車與交通　0 - 29%

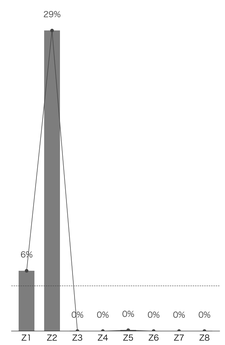

醫療／文教　0 - 23%

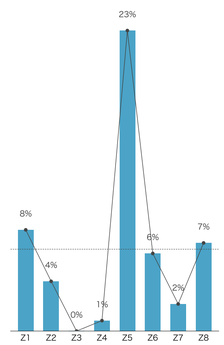

運動休閒　0 - 14%

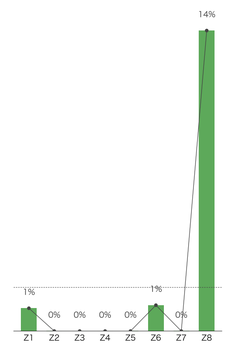

公園綠地（佔分區土地）　2 - 20%

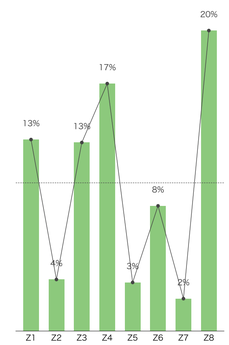

平面停車場（佔分區土地）　0.2 - 5.2%

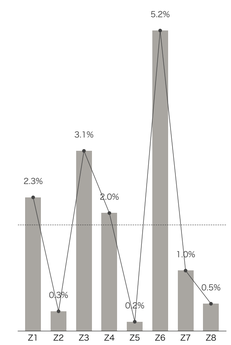

汽車格密度（格／ha）　22 - 74