N

1:8,000

0 100 200 500 1,000 m

市民大道沿線｜歷史圖資痕跡疊圖

200 m 方格中，現況街廓佔 30% 以上者置入當年地圖（反黑），其餘為現況圖底（諾利圖）；淡水河堤外不置入。

1904

日治臺灣堡圖（明治版）

原圖 1:20,000

可見痕跡

水圳、埤塘（上埤頭）、鐵道

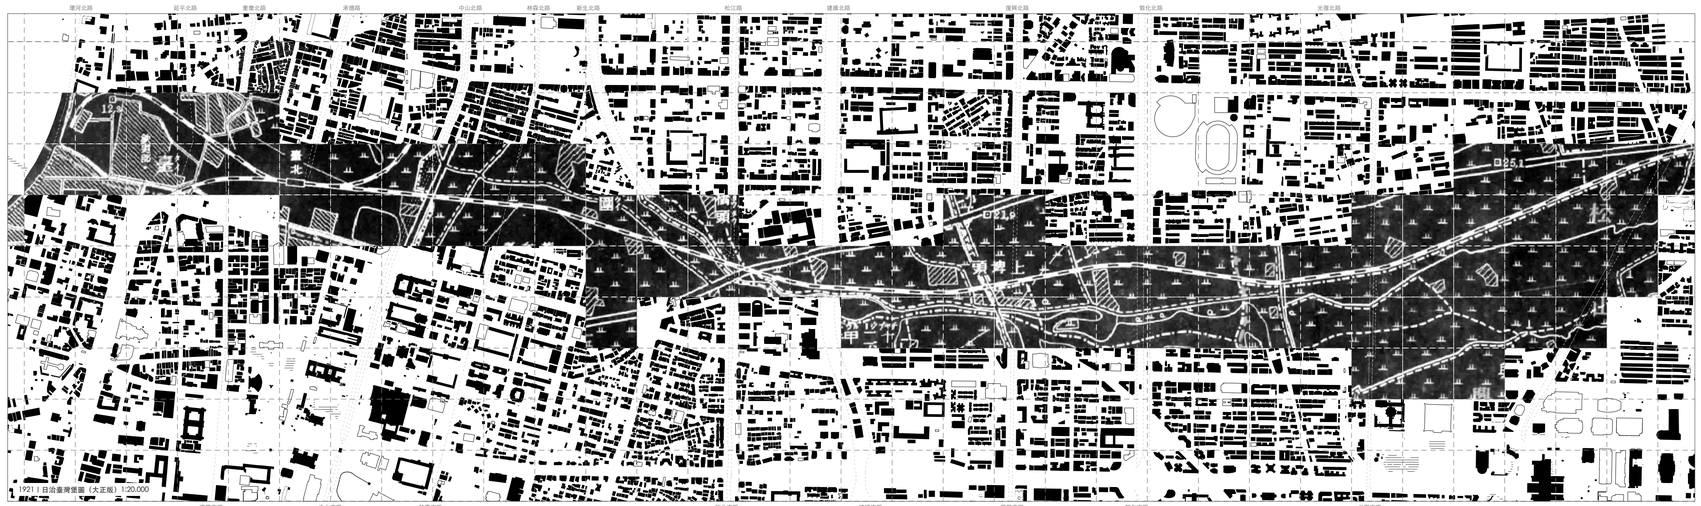

1921

日治臺灣堡圖（大正版）

原圖 1:20,000

可見痕跡

水圳、埤塘、鐵道——與 1904 對照

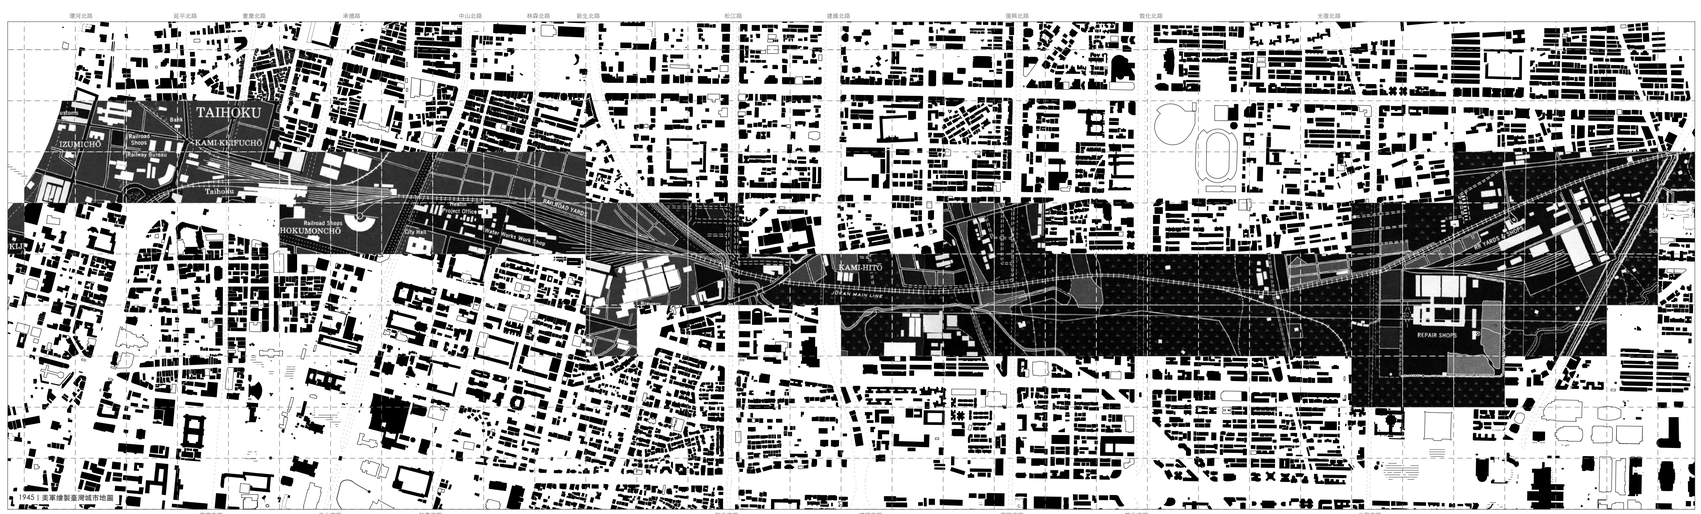

1945

美軍繪製臺灣城市地圖

可見痕跡

縱貫線、調車場、鐵道部、機廠、酒廠

當年地圖（反黑）

現況圖底（諾利圖）

200 m 方格

1:12,000（A1）

0 250 500 1000 m

N

資料：中央研究院人社中心 臺灣百年歷史地圖（JM20K_1904、JM20K_1921、AMCityPlan_1945）；現況圖底 © OpenStreetMap contributors

計畫範圍與都市發展、都更案例

建物依所屬行政區（通盤檢討細部計畫範圍）著色，紅→藍由西向東；區界內縮拉開、不繪道路，留白即街道。黑線＝市民大道。都更與發展案例以單一深色剪影、基地範圍及編號標示，編號由西向東，案件狀態見下方說明。

格網北

計畫範圍　大同區 P110002　萬華區 P110001　中正區 P111021　中山區 P110025　大安區 P110013　松山區 P108012　信義區 P112014　市民大道　案例　建物剪影　敷地／裙樓　基地範圍　基地概括／推估（虛線）　1 案件編號　結案未續行

1:8,699　0　500　1000 m

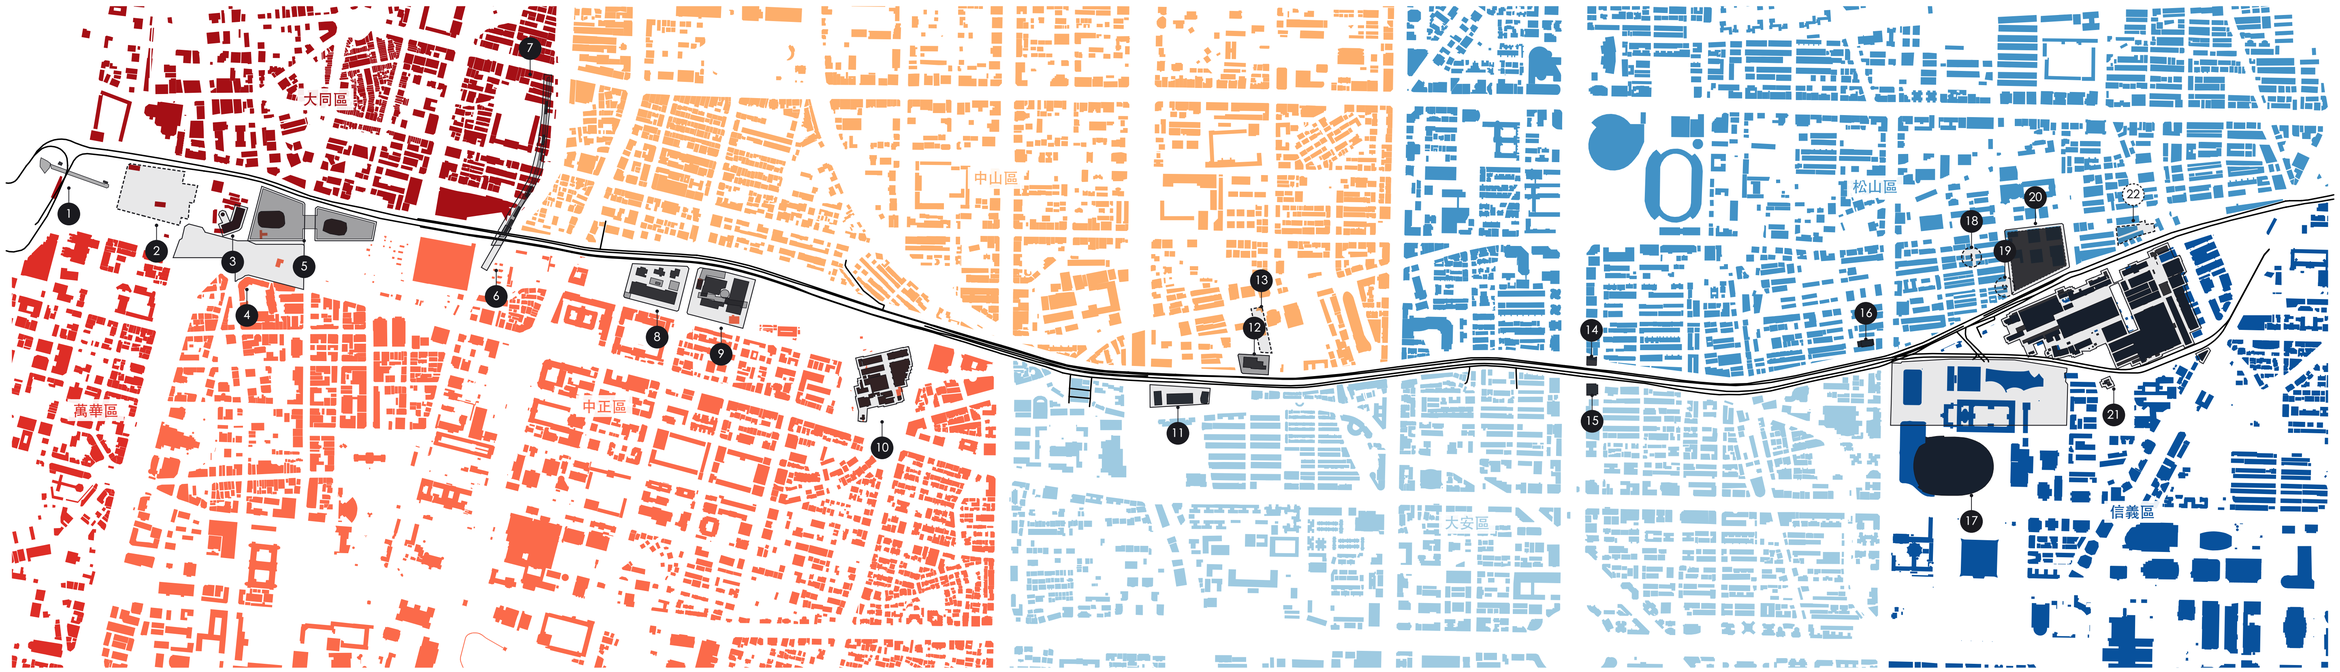

S1 西端車站段	S2 華山行政段	S3 生活街區段	S4 敦化辦公段	S5 文體與機廠段
環河北路—中山北路	中山北路—新生北路	新生北路—復興南路	復興南路—光復南路	光復南路—基隆路

各段更新意圖

S1 西端車站段

環河北路—中山北路｜大同、中正

鐵路地下化釋出土地轉為交通、辦公、博物館核心；古蹟活化重建歷史地景。

S2 華山行政段

中山北路—新生北路｜中正、中山

南側強化中央行政、保留文創街廓；北側六條通升格商業；行二行三公辦都更。

S3 生活街區段

新生北路—復興南路｜中山、大安

不增容積、放寬使用並劃定更新地區；以開放空間換獎勵，形塑東西向景觀軸。

S4 敦化辦公段

復興南路—光復南路｜松山、大安

維持辦公金融特性；沿市民大道放寬支援性商業，TOD 引導站點周邊加密。

S5 文體與機廠段

光復南路—基隆路｜信義、松山

工業遺址轉文化體育與商業；老舊社區公辦都更；松山車站為東區轉運門戶。

案件狀態說明｜依所在分段排列

推動階段：規劃中 → 前期／招商 → 審議中 → 審議通過 → 施工中／展延 → 已完成；另列 結案未續行。★＝推定待核

1 玉泉公園人本跨橋　［規劃中］

公共工程｜水利處｜堤內外人行與自行車跨橋，含電梯、階梯與牽引道；把西端車站區接回淡水河水岸，尚非定案構線。

2 臺北車站 E1／E2　［審議中］

公有地都更｜鐵道局｜鐵道局公有地都更，更新單元 17 筆約 1.6 ha，位於北門與車站西側；2023 報核、2024 公展，考古試掘與文資修復同步進行。未來為博物館特專區＋商業，臨鄭州路留 10 m 帶狀開放空間。

3 鐵道部園區（鐵道博物館）　［已完成］

文資｜臺博館｜臺灣總督府交通局鐵道部古蹟修復為鐵道歷史博物館（2020 開館）。

4 北門廣場　［已完成］

公共空間｜市府｜忠孝橋引道拆除後重現北門城與城牆地景（2017）；與鐵道部、三井倉庫串成北門文資節點。

5 臺北雙子星（C1／D1）★　［施工中／展延］

聯合開發｜機捷｜機捷臺北站上方聯開，C1 55F 辦公商城、D1 74F 企業總部＋旅館＋觀景台，裙樓設國門客廳並跨重慶北路相連；預計 116 年完工。塔樓剪影取自 OSM 興建中輪廓（D1 約 3,340 ㎡、C1 約 2,480 ㎡）；跨重慶北路之連續裙樓依展覽模型推估。

6 跨市民大道空廊（Skywalk）★　［前期／招商］

公共工程｜臺北捷運公司｜城市大道計畫之跨市民大道段（發包中）：連續空廊、大尺度行人穿越道與頂棚，自心中山南端跨越市民大道接臺北車站，模型顯示步行平台穿越高架橋下。位置依心中山軸線南延推估。

7 心中山線形公園　［已完成］

公共空間｜北捷｜城市大道（Skywalk）計畫之公園段，2025-08 完工；捷運淡水線上方線形公園，南端 R1 出入口緊鄰市民大道。

8 台灣心 HUB（行二行三）　［審議通過］

公辦｜住都中心／冠德｜住都中心公辦、冠德出資，基地 18,365 ㎡；辦公棟 22F（88.6 m）、住宅棟 24F（89.6 m），預計 2031 完工。現住戶原地安置；「台北心軸線」New Civic Hub 核心，與南側司法園區隔市民大道相對。

9 華山司法園區　［施工中／展延］

公共建設｜司法院｜華山行六用地司法機關遷建；2022 先期工程動土，期程展延。完工後南側新增大量公務人流。

10 華山 1914 文創園區　［已完成］

文資｜文化部｜創意文化專用區內之酒廠古蹟群，假日文創人流核心。

11 明日博／懷生段931　［已完成］

私人｜「臺北好好看」｜「臺北好好看」專案，市民大道三段×建國南路，東西兩基地約 0.9 ha，2016 完成；以廣場式開放空間、地面人行通道換取容積獎勵，是沿線少數已兌現的地面開放空間樣本。

12 長安市民公辦都更　［審議中］

公辦｜住都中心／潤泰｜住都中心公辦、潤泰創新實施，5 筆約 0.45 ha；2025-11 公展、12 月公辦公聽會，審議中。23 層住宅，1F 托嬰中心＋店鋪，臨市民大道退縮約 17 m 開放空間（建蔽約 35%）。

13 中油中山公辦都更　［前期／招商］

公辦｜前期｜原中油加油站用地（P092003／P093011 變更），4 筆約 0.41 ha；2026-05 選定公辦都更，招商準備中、尚無配置。位於市民大道與八德路之間，可能改變南北穿越路徑。

14 德杰（敦化×市民 東北）★　［已完成］

私人｜德杰案，延吉段三小段 831-1 等，敦化×市民東北角；已完成並成果備查。剪影以東北角 22F 敦南樓苑推定，待核。

15 富邦（敦化×市民 東南）　［已完成］

私人｜富邦案，仁愛段六小段 245-2 等，敦化×市民東南角；已完成（富邦敦南大樓）。與 U05 分屬道路兩側，可比較不同退縮與商業介面。

16 麗寶（光復×市民 西北）　［已完成］

私人｜麗寶案，延吉段一小段 175 等，光復×市民西北角；已完成並成果備查，代表光復節點既有更新成果。

17 臺北大巨蛋／松菸　［已完成］

BOT｜市府｜松菸特專區之大巨蛋（2023 啟用）與松山文創園區；平日中等、活動散場為極端尖峰。

18 青園（光復 13、17 巷）　［審議中］

私人｜申請審查｜青園案，西松段三小段 281 等 18 筆，光復南路 13、17 巷；2026 申請審查、尚未核定。後續看更新範圍與巷道通行設計。

19 旭豐（八德 72、106 巷）　［審議中］

私人｜申請審查｜旭豐案，西松段三小段 454 等 43 筆，八德路 72、106 巷；2026-06 申請審查，舊事業概要與本次申請需分開辨識。

20 京華城重建 ★　［施工中／展延］

私人｜威京｜原唐榮鐵工廠商三（特）基地重建為大型商業辦公；土地扣押中、變更設計待審，無公開配置。量體以基地內縮 8 m 示意（虛線）。

21 臺北機廠（國家鐵道博物館）★　［施工中／展延］

文資｜文化部｜國定古蹟臺北機廠轉為國家鐵道博物館園區，分期修復開放；與大巨蛋形成南北軸。

22 機廠北側 7599　［結案未續行］

公辦｜已停止｜公辦案，西松段三小段 58 等 33 筆約 0.39 ha，臺北機廠北側；2025-10 因所有權人意願未達門檻結案。保留對照，顯示小街廓整合困難。

資料：臺北市都發局歷年計畫索引與各區通盤檢討（查詢 2026-10-05）；案件階段沿用《簡要標記 v2》《公共都更與公共建設編號圖》並補展覽資料（2026-10-04）；建物：統一清理 v2 擴幅建物輪廓；表現法參考 Architecture Workroom Brussels, Thinkers versus Makers (2016)。底圖 © OpenStreetMap contributors / ODbL

都市計畫個案 × 公告當年航照

紅框內為該案公告當年之臺北市正射影像（黑白）；當年無影像者取最近一年。

都市計畫個案範圍　　行政區通檢範圍界　　幹道

格網北

0　500　1000 m

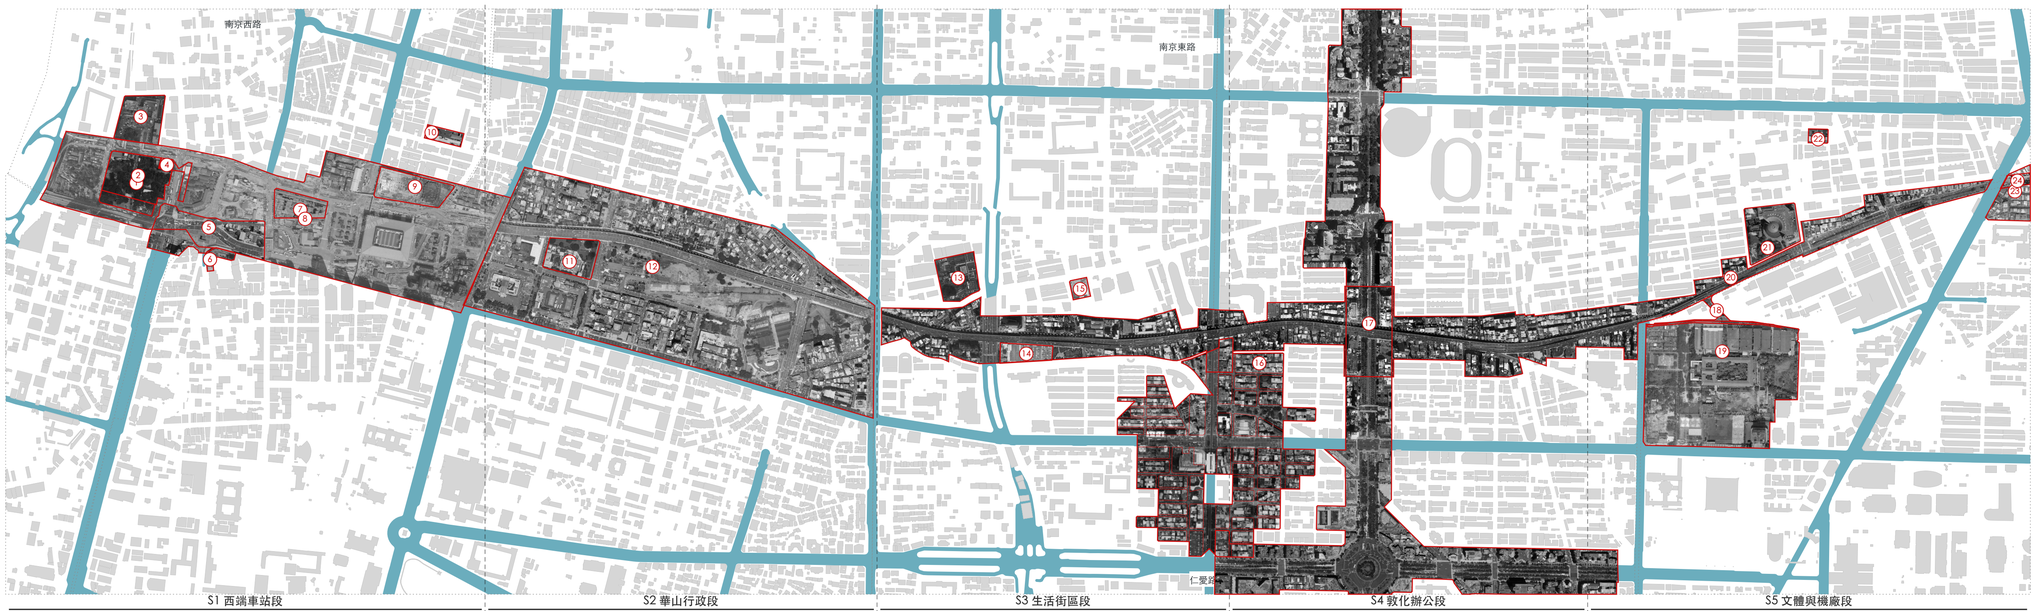

S1 西端車站段
環河北路—中山北路

S2 華山行政段
中山北路—新生北路

S3 生活街區段
新生北路—復興南路

S4 敦化辦公段
復興南路—光復南路

S5 文體與機廠段
光復南路—基隆路

各段更新意圖

S1 西端車站段
環河北路—中山北路｜大同、中正

鐵路地下化釋出土地轉為交通、辦公、博物館核心；古蹟活化重建歷史地景。

S2 華山行政段
中山北路—新生北路｜中正、中山

南側強化中央行政、保留文創街廊；北側六條通升格商業；行二行三公辦都更。

S3 生活街區段
新生北路—復興南路｜中山、大安

不增容積、放寬使用並劃定更新地區；以開放空間換獎勵，形塑東西向景觀軸。

S4 敦化辦公段
復興南路—光復南路｜松山、大安

維持辦公金融特性；沿市民大道放寬支援性商業，TOD引導站點周邊加密。

S5 文體與機廠段
光復南路—基隆路｜信義、松山

工業遺址轉文化體育與商業；老舊社區公辦都更；松山車站為東區轉運門戶。

紅框一覽

①	2019	E1／E2 細部｜博物館特專區
②	2018	E1／E2 主要｜公設用地轉特專區
③	2026	中興醫院｜地下連通北門站（影像 2025）
④	2004	北門站｜捷運出入口
⑤	2016	北門廣場｜拆引道
⑥	2007	郵電大樓｜古蹟保存
⑦	2006	C1／D1 雙子星｜聯合開發
⑧	1993	臺北車站特專區｜交通運輸中心
⑨	2004	交九｜轉運站
⑩	2002	當代館｜舊市府活化
⑪	2022	行二行三｜中央行政主體
⑫	2003	華山整體計畫｜行政／文創專用區
⑬	2025	工業區轉大學用地
⑭	2004	懷生段｜開放空間換容積
⑮	2003	中油加油站｜轉作住商或公園
⑯	2019	TOD｜站點周邊加密
⑰	2002	敦化特專區｜辦公金融
⑱	2010	松菸北側｜工業區改道路
⑲	2003	松菸特專區｜大巨蛋
⑳	2008	市民大道兩側｜放寬使用
㉑	2014	唐榮／京華城｜商業多目標
㉒	2020	西松段｜老舊社區更新
㉓	2004	松山車站｜東區轉運樞紐
㉔	2001	南港專案｜鐵路地下化東延

影像：臺北市歷史圖資展示系統（1994–2025）｜計畫：臺北市都發局都市計畫書｜底圖 © OpenStreetMap contributors

市民高架沿線｜一樓使用現況

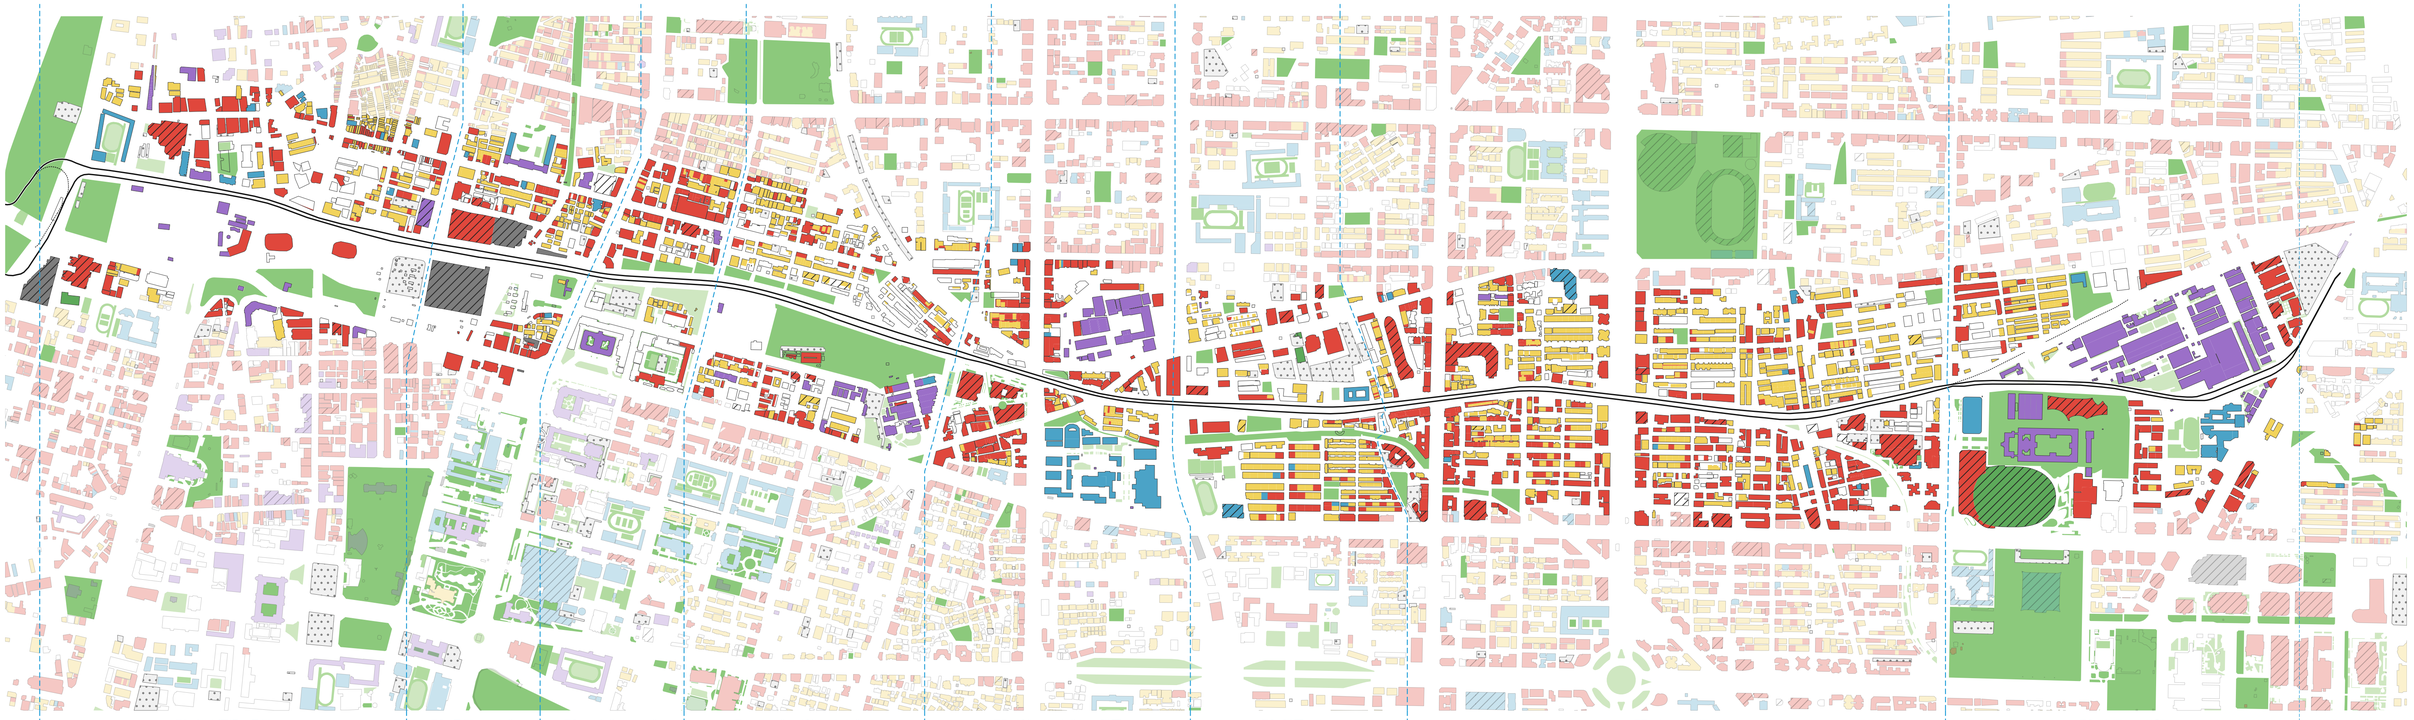

住宅
商業
產業與古蹟
停車與交通
醫療／文教
運動休閒
公園
草地／樹林
運動場／遊戲場
平面停車場
含停車場之建物
市民高架
匝道
設計介入單元 Z1 - Z8
高架兩側 300 m 範圍
範圍外

0 250 500 1000 m

各用途於 Z1 - Z8 的變化

住宅　12 - 47%

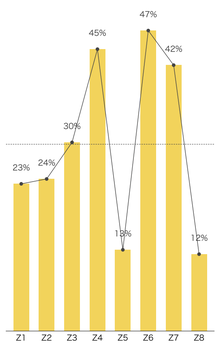

商業　29 - 61%

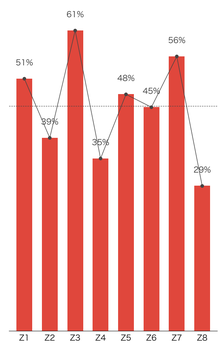

產業　0 - 38%

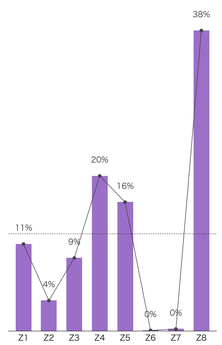

停車與交通　0 - 29%

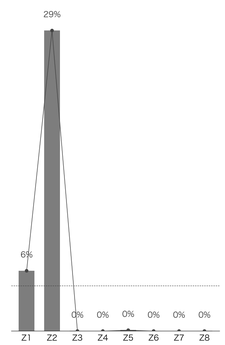

醫療／文教　0 - 23%

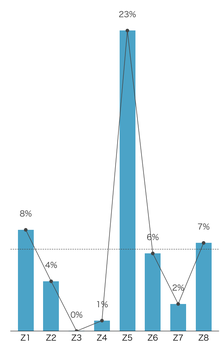

運動休閒　0 - 14%

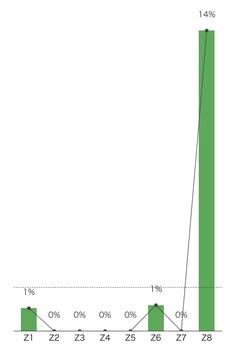

公園綠地（佔分區土地）　2 - 20%

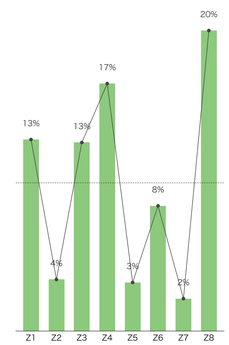

平面停車場（佔分區土地）　0.2 - 5.2%

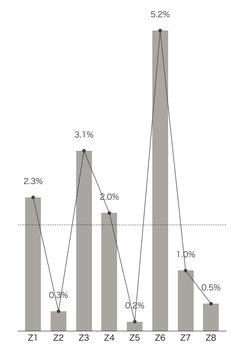

汽車格密度（格／ha）　22 - 74

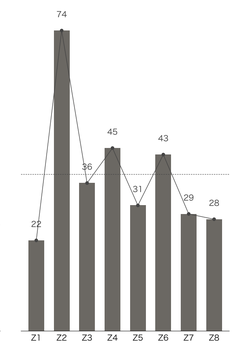

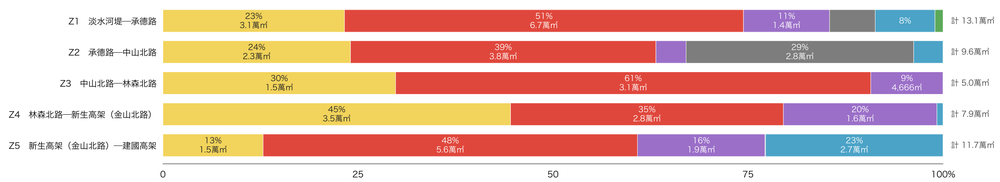

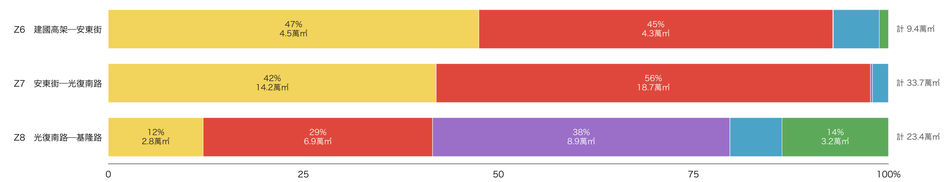

市民高架沿線｜商業、產業與停車

市民高架
設計介入單元界線 Z1 - Z8
其他建物
範圍外
市民大道地下停車場
停車場出入口
停車場建物
路外停車場（圓大小＝汽車格數）
路邊汽車格

商業｜一樓店面＋商業＋辦公

一樓店面 23.6%　商業 17.4%　辦公 1.3%

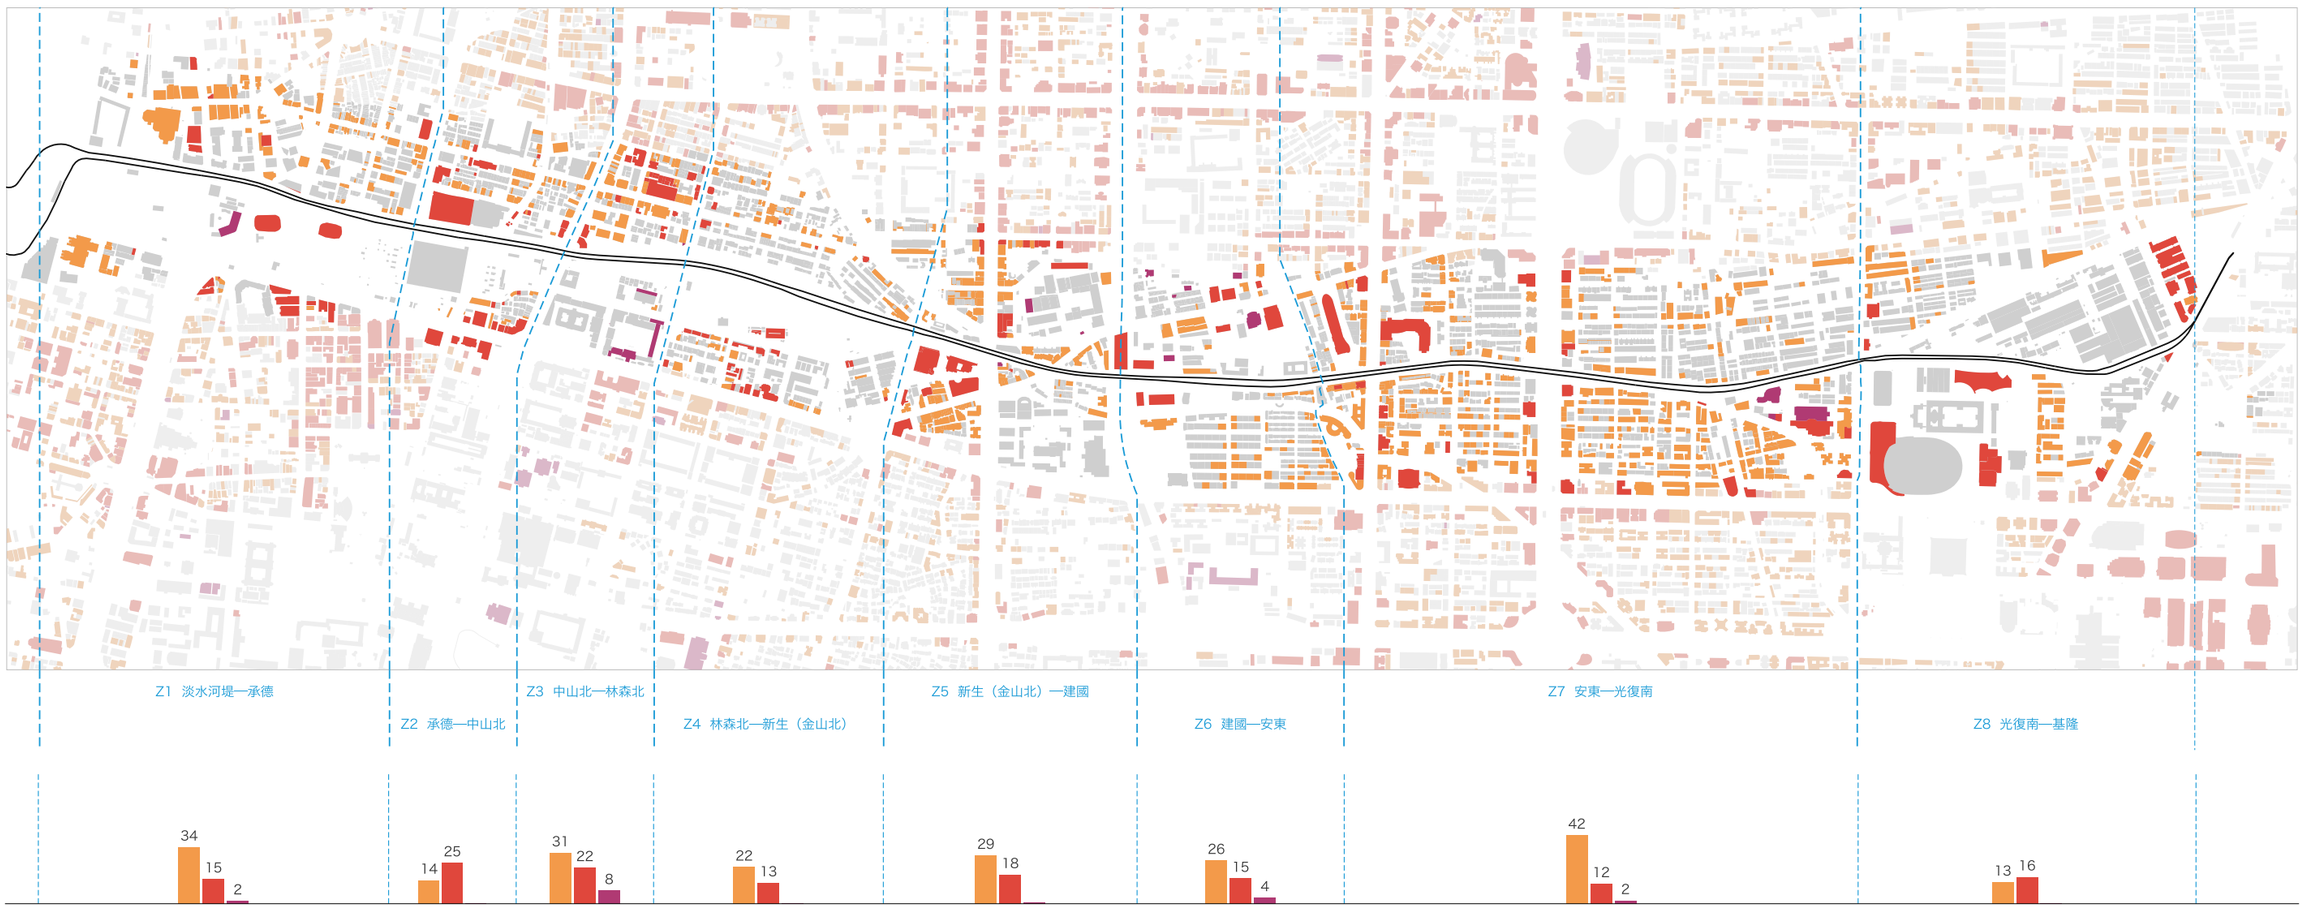

產業｜工業倉儲＋登錄古蹟・歷史建築

工業／倉儲 0.5%　產業遺構／登錄古蹟・歷史建築 6.2%

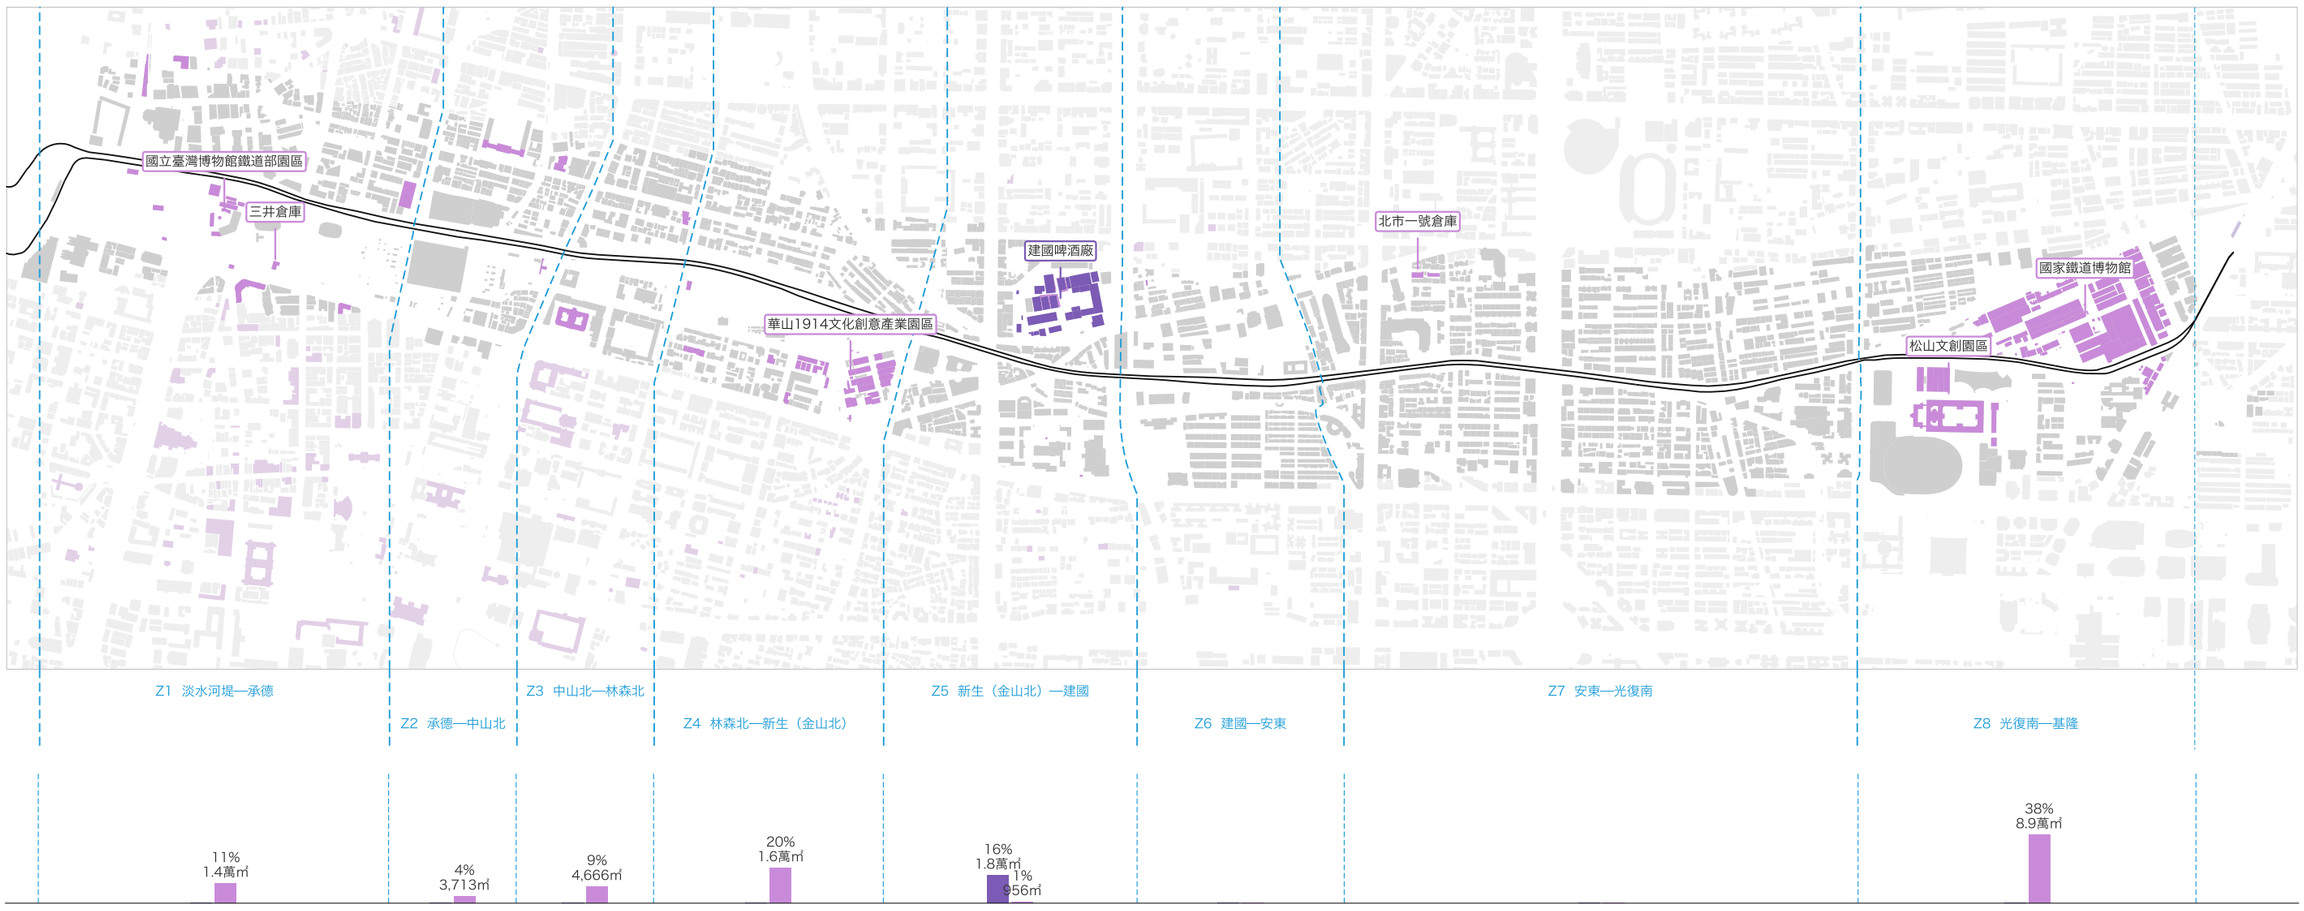

停車與交通

交通／停車 1.4%

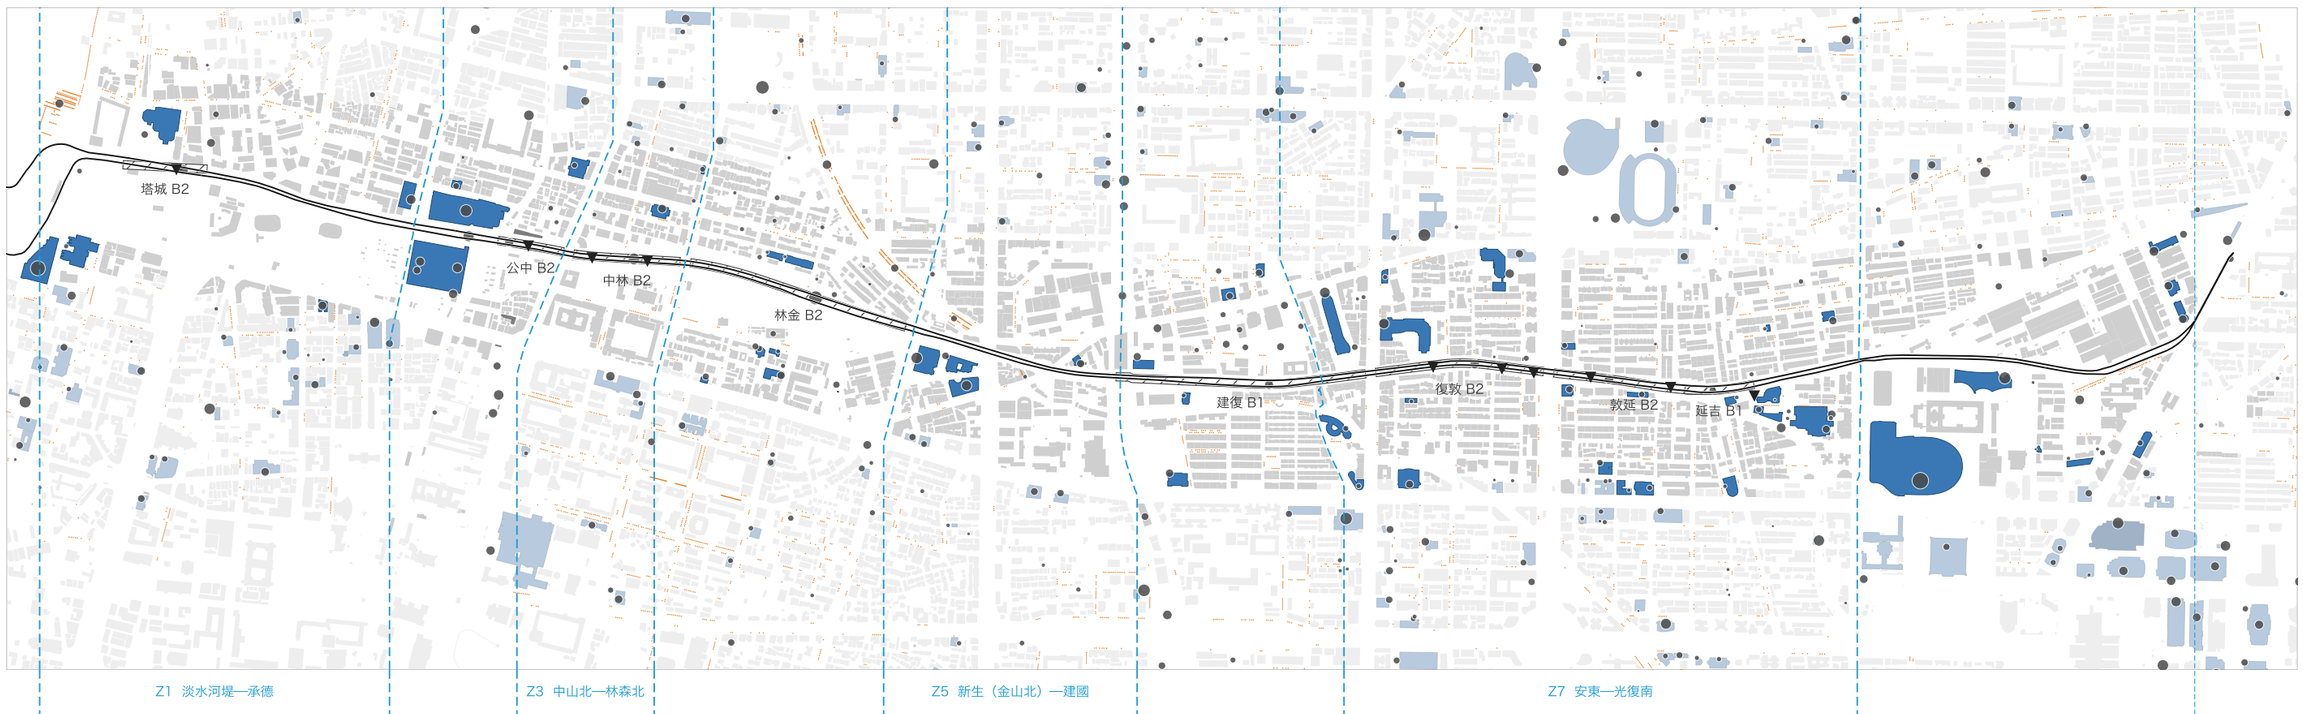

市民高架沿線｜居住、醫療文教與開放空間

市民高架
設計介入單元界線 Z1 - Z8
其他建物
範圍外
市民大道地下停車場
停車場出入口
停車場建物
路外停車場（圓大小＝汽車格數）
路邊汽車格

住宅

住宅 25.6%

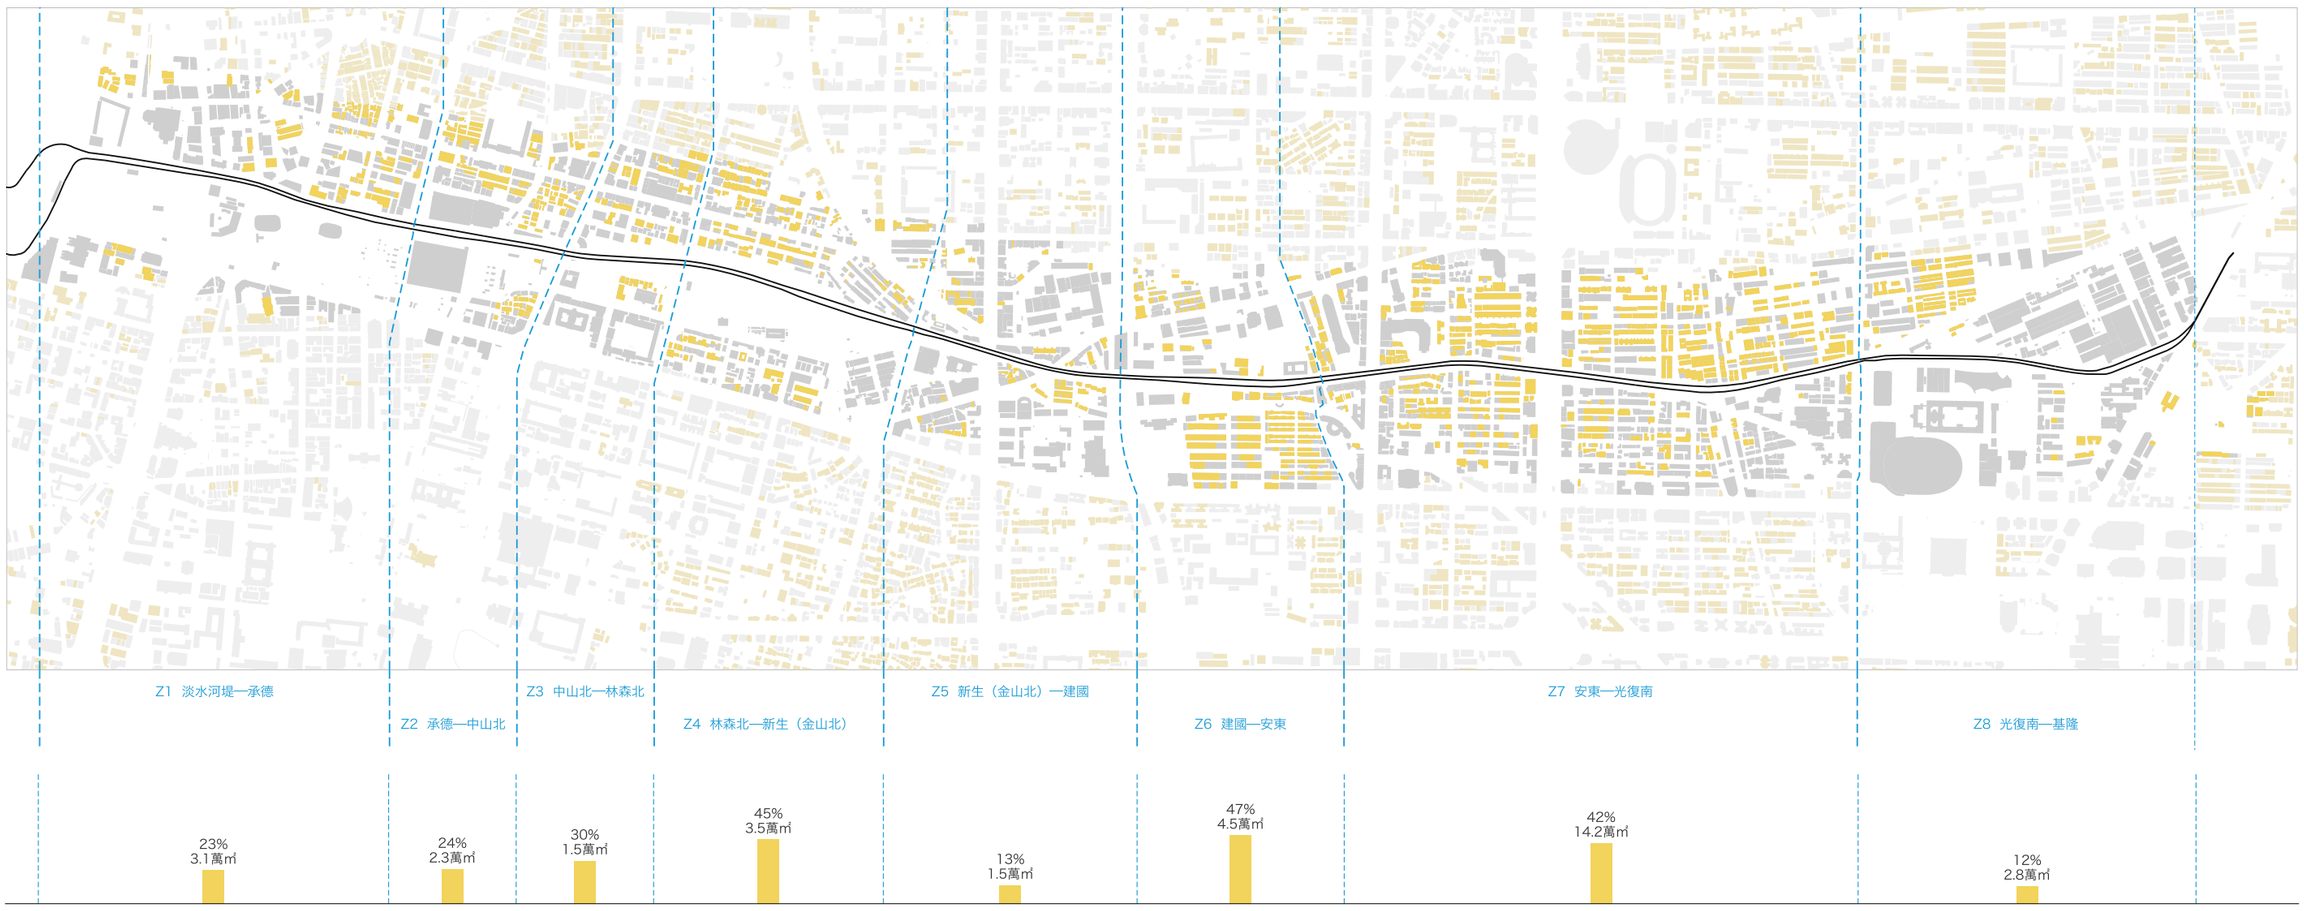

醫療＋文教

醫療 2.6%　文教 6.1%

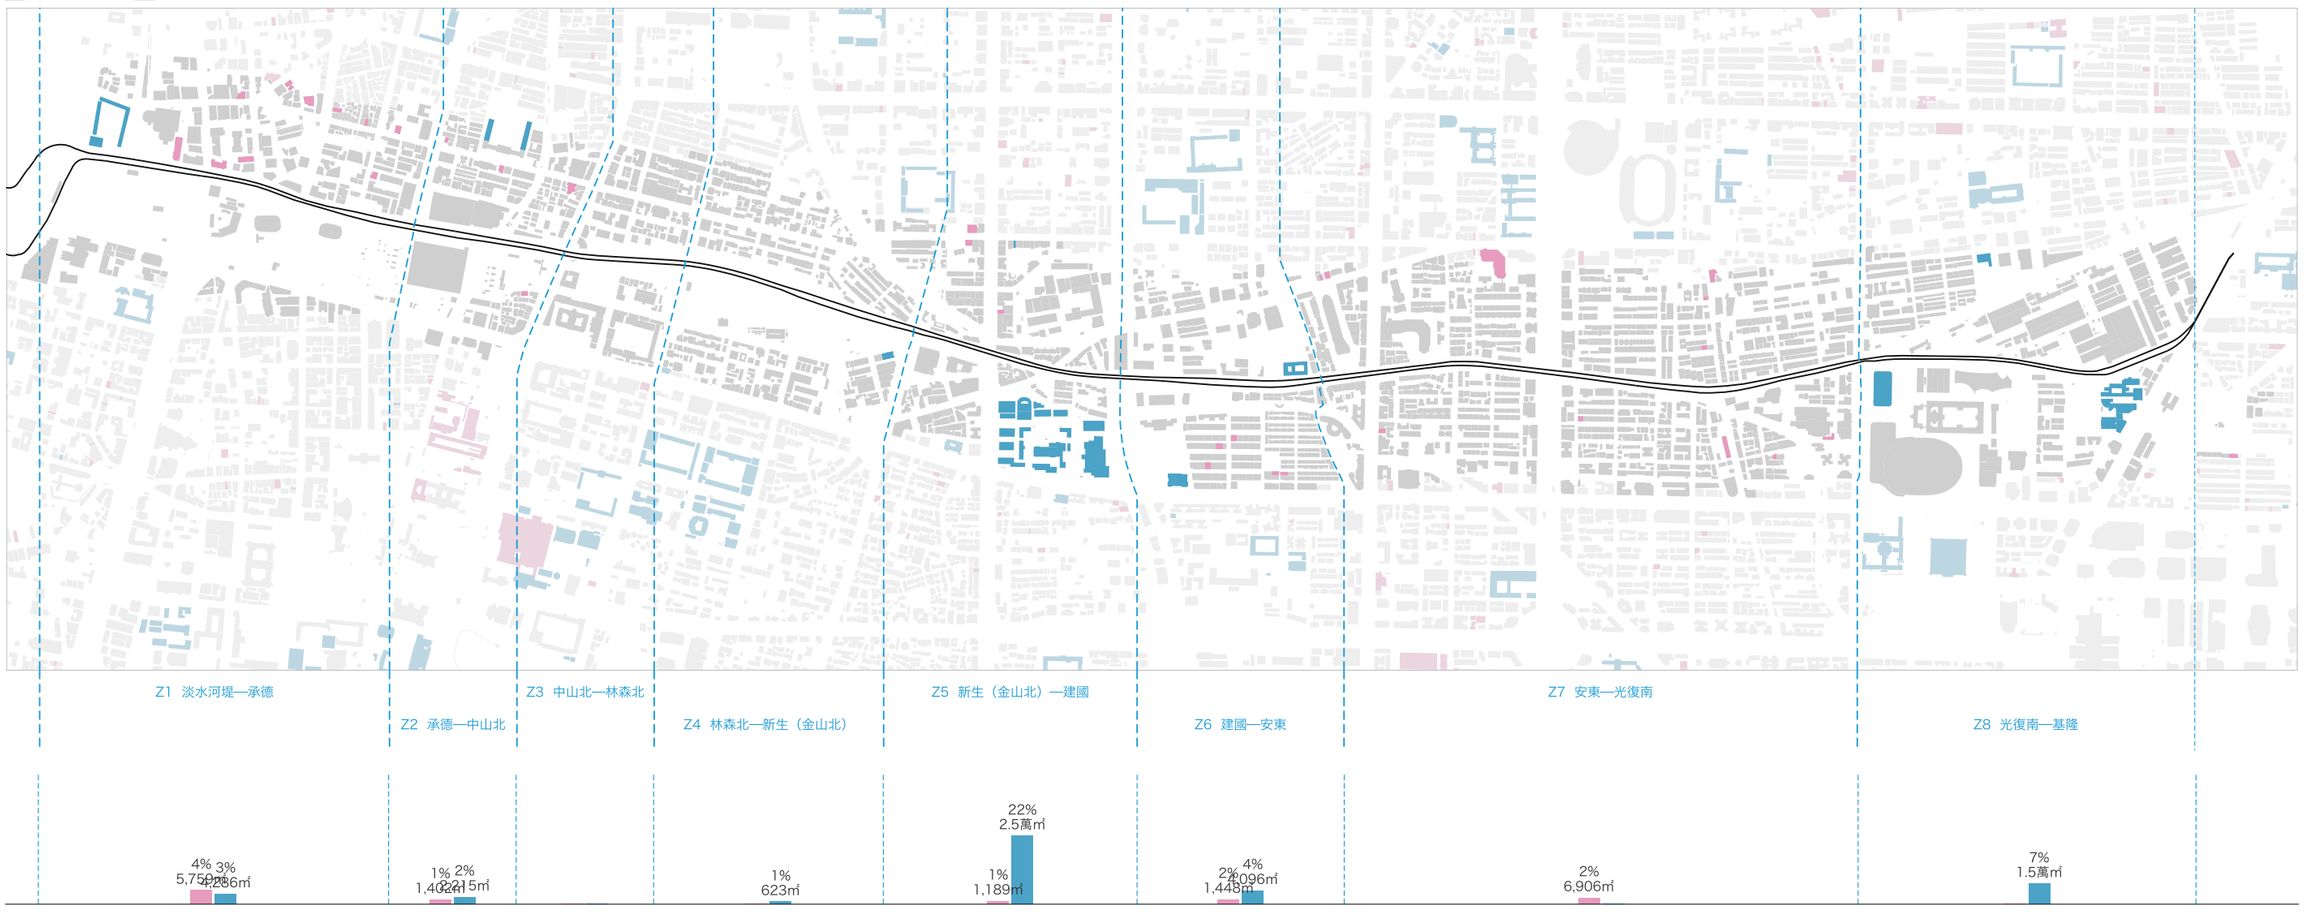

運動休閒＋公園綠地

運動休閒 2.0%　公園綠地（佔土地）

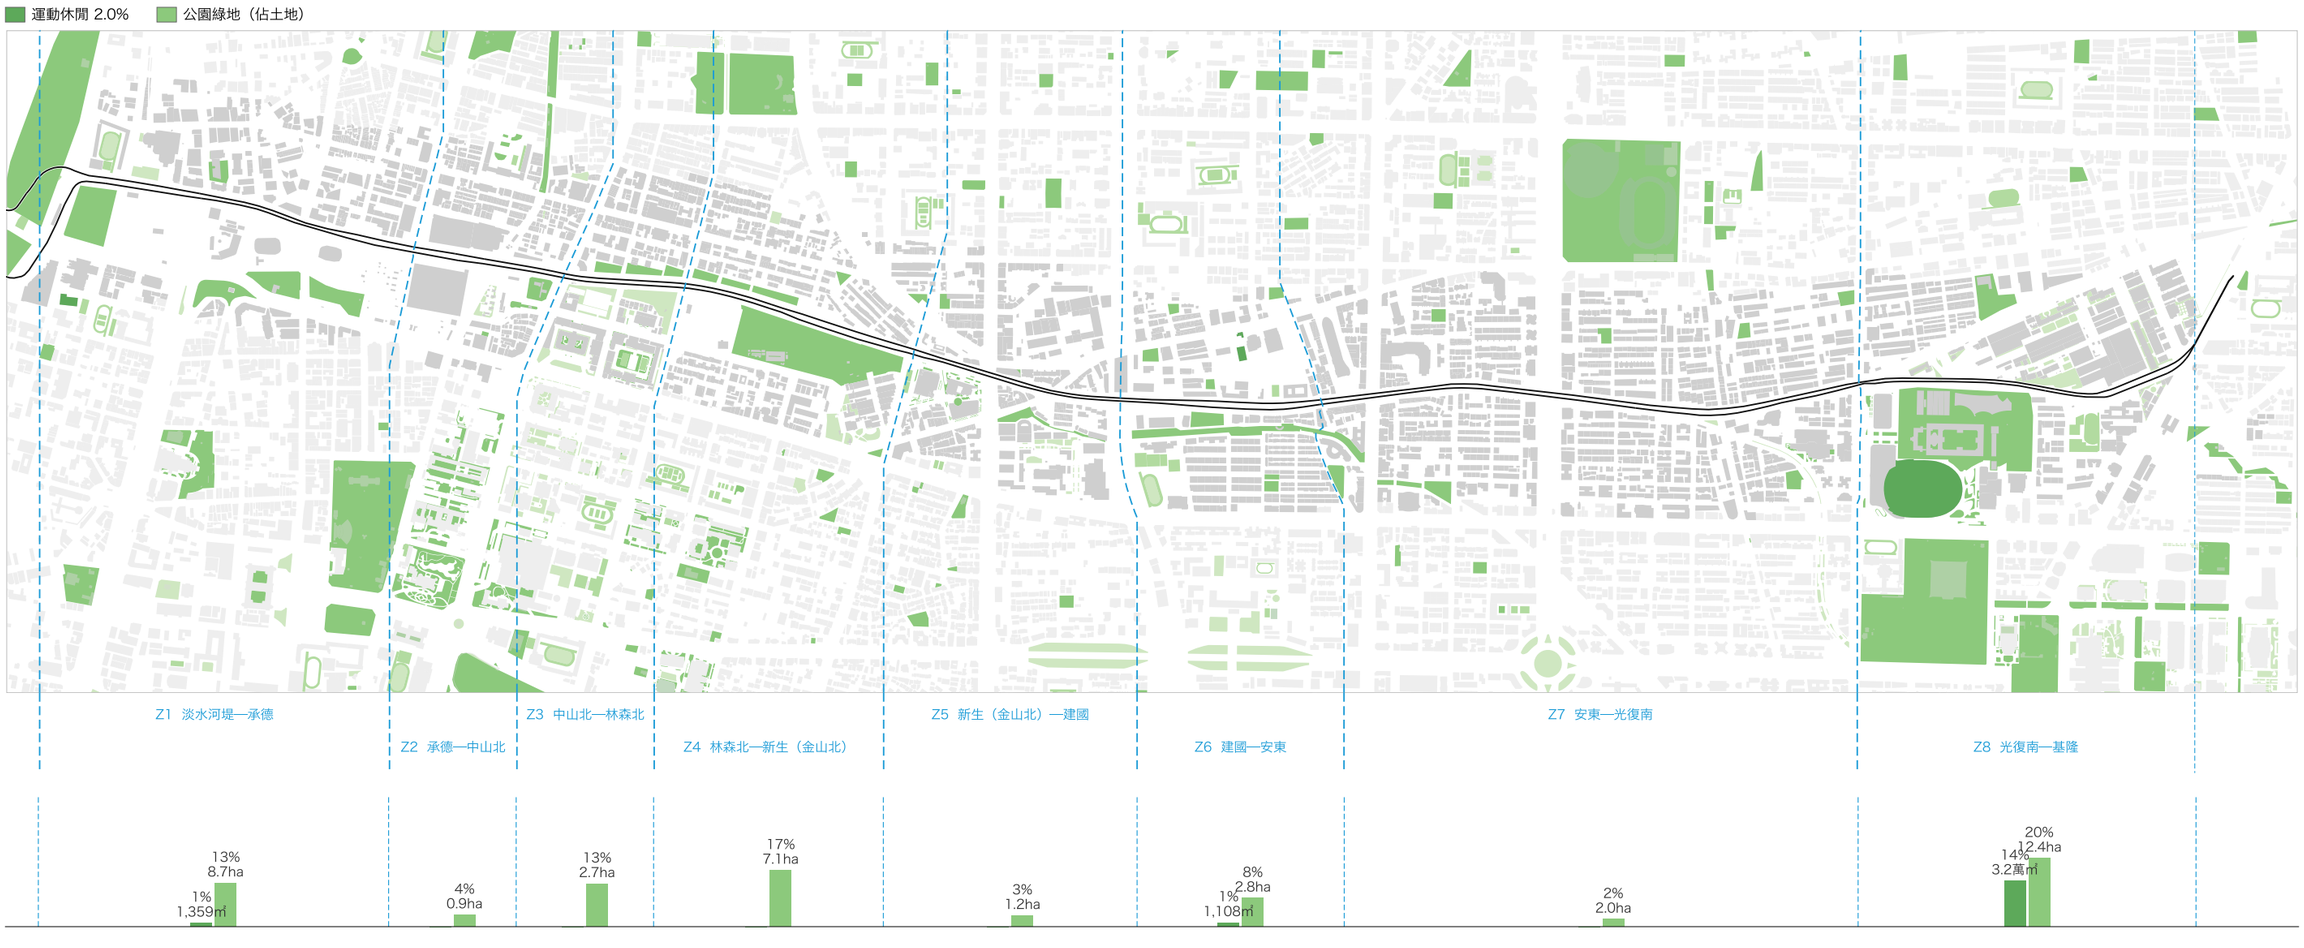

設計介入單元 Z1 - Z8｜建物組成

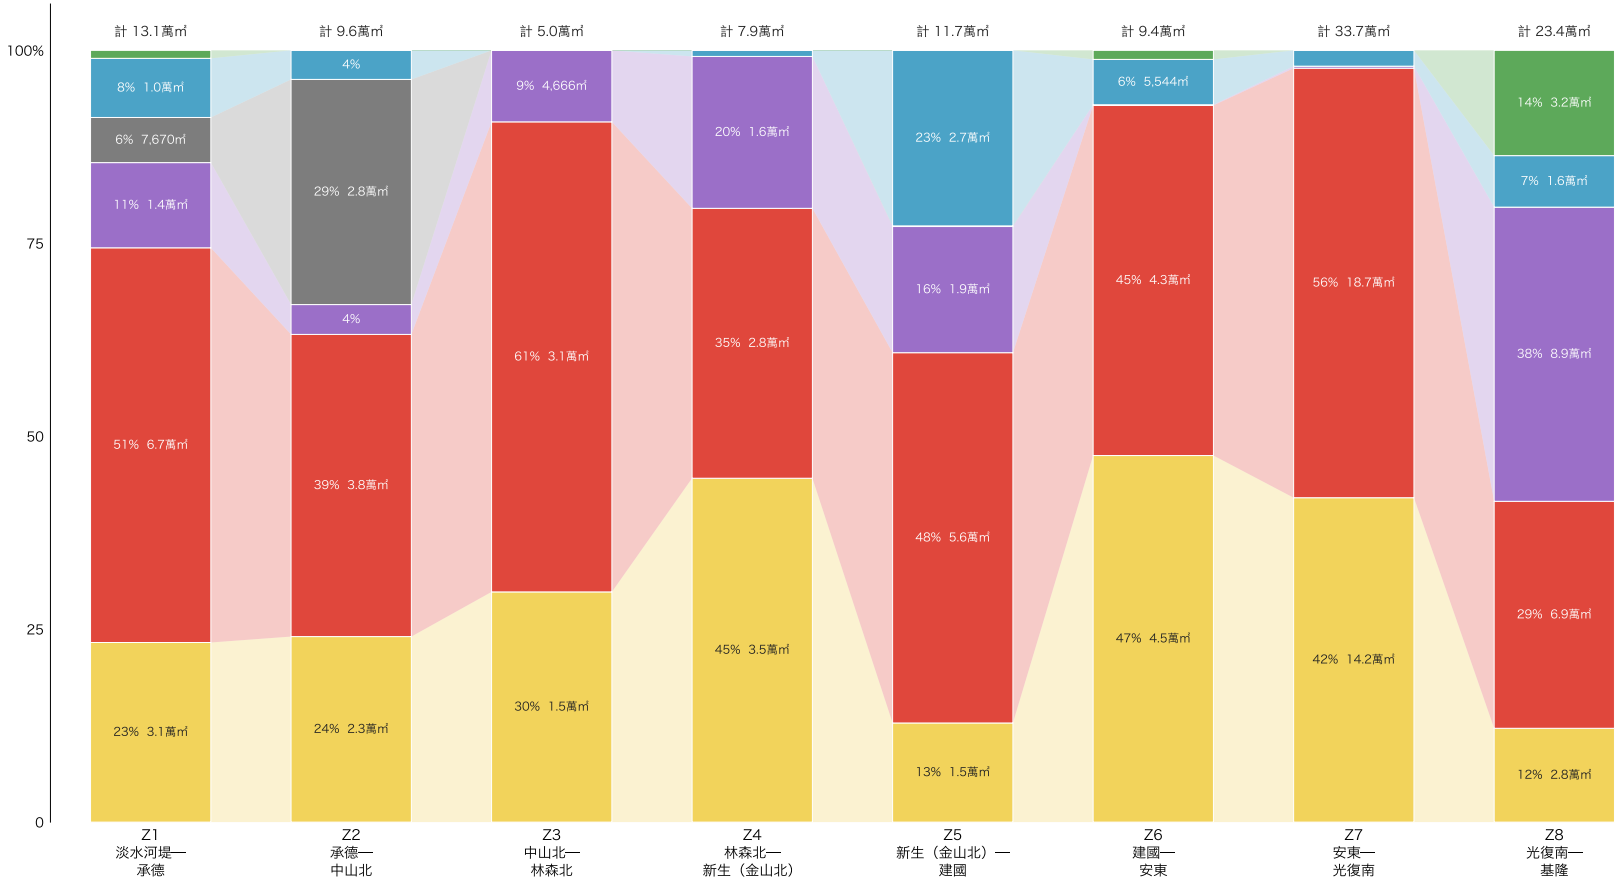

運動休閒
醫療／文教
停車與交通
產業與古蹟
商業
住宅

Z1 淡水河堤—承德｜河岸門戶＋北門古蹟群＋台北雙子星
Z2 承德—中山北｜臺北車站樞紐
Z3 中山北—林森北｜行政院行二行三公辦都更
Z4 林森北—新生（金山北）｜華山
Z5 新生（金山北）—建國｜光華—北科大—建國啤酒廠
Z6 建國—安東｜長安段公辦都更
Z7 安東—光復南｜東區北緣宵夜／居酒屋餐飲帶
Z8 光復南—基隆｜松山文創＋大巨蛋＋國家鐵道博物館

停車｜汽車格（深灰）／路外機車格（淺灰）

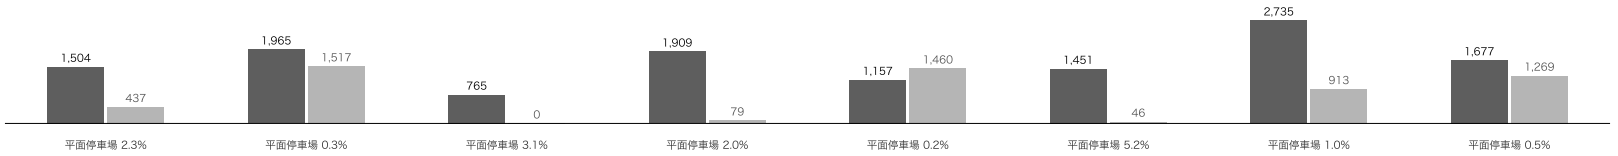

Z1　淡水河堤—承德路｜南北通行元素與特性建築

主角：河岸門戶＋北門古蹟群＋台北雙子星｜1:4,200（A3）｜圖例見共用圖例

0　50　100　200　400　m　1:4,200（A3）

N

Z1　淡水河堤—承德路｜南北通行元素與特性建築

圖例與說明（配合 A3 圖面，1:4,200）

圖例

+2 高架

市民高架

+1 天橋

人行天橋（承德路）

±0 地面

特性建築

建物

可通過路口

道路與人行道

B1 地下一層

北門站、台北車站地下通廊、機捷站體（大廳）

B2 地下二層

台北地下街（Y區）、機捷月台

地下層：大道下方較暗、街廓內較亮

單元界線

單元外

通行元素

項目	說明
平面穿越	6 處：環河北、西寧北、塔城、延平北、重慶北、承德
地下街與站體	北門站、機捷 A1、台北地下街 Y 區、台北車站地下通廊
人行天橋	承德路
穿越間距	141／221／149／135／319 m
最長無穿越段	319 m（重慶北—承德，僅地下街可過）

特性建築

項目	說明
河岸門戶	B02 跨堤橋、西寧國宅、忠孝抽水站
北門古蹟群	北門、臺北郵局、三井倉庫、撫臺街洋樓、鐵道部園區、台鐵舊禮堂、專賣局後站倉庫
台北雙子星	C1／D1（興建中）
公辦都更	U01 E1／E2 特定專用區
界面大型建物	中興醫院、皇翔臺北廣場 等

判準：河岸門戶、北門古蹟群、台北雙子星，及公辦都更與界面大型建物

資料：臺北三維模型（2017）、OSM、財政部稅籍登記、臺北市正射影像 2025 | © OpenStreetMap contributors

Z2　承德路—中山北路｜南北通行元素與特性建築

主角：臺北車站樞紐（車站、京站、轉運站、心中山）｜1:4,200（A3）｜圖例見共用圖例

0　50　100　200　400　m　1:4,200（A3）

N

Z2　承德路—中山北路｜南北通行元素與特性建築

圖例與說明（配合 A3 圖面，1:4,200）

圖例

+2 高架

市民高架

+1 天橋

人行天橋（承德路天橋）

±0 地面

源頭建築（流向臺北車站的人群）

目的地：臺北車站

建物

可通過路口

道路與人行道

B1 地下一層

台北車站地下通廊（北側）、
捷運台北車站（北端大廳）、
台北車站地下通廊（東側）、
中山地下街（R區）

B2 地下二層

台北地下街（Y區）

地下層：大道下方較暗、街廊內較亮

單元界線

單元外

通行元素

項目	說明
平面穿越	1 處：中山北路
地下街與站體	台北地下街 Y 區（B2）、台北車站地下通廊、北端大廳、中山地下街 R 區（B1）
人行天橋	承德路
最長無穿越段	419 m

判準：流向臺北車站人群的源頭建築；淡酒紅為目的地臺北車站

資料：臺北三維模型（2017）、OSM、財政部稅籍登記、臺北市正射影像 2025｜© OpenStreetMap contributors

Z2　承德路—中山北路｜源頭建築｜流向臺北車站的人從哪裡來

判準：總樓地板 ≥ 1 萬㎡（轉乘設施不設門檻）；編號＝樓地板由大到小，對應 A1 酒紅剪影

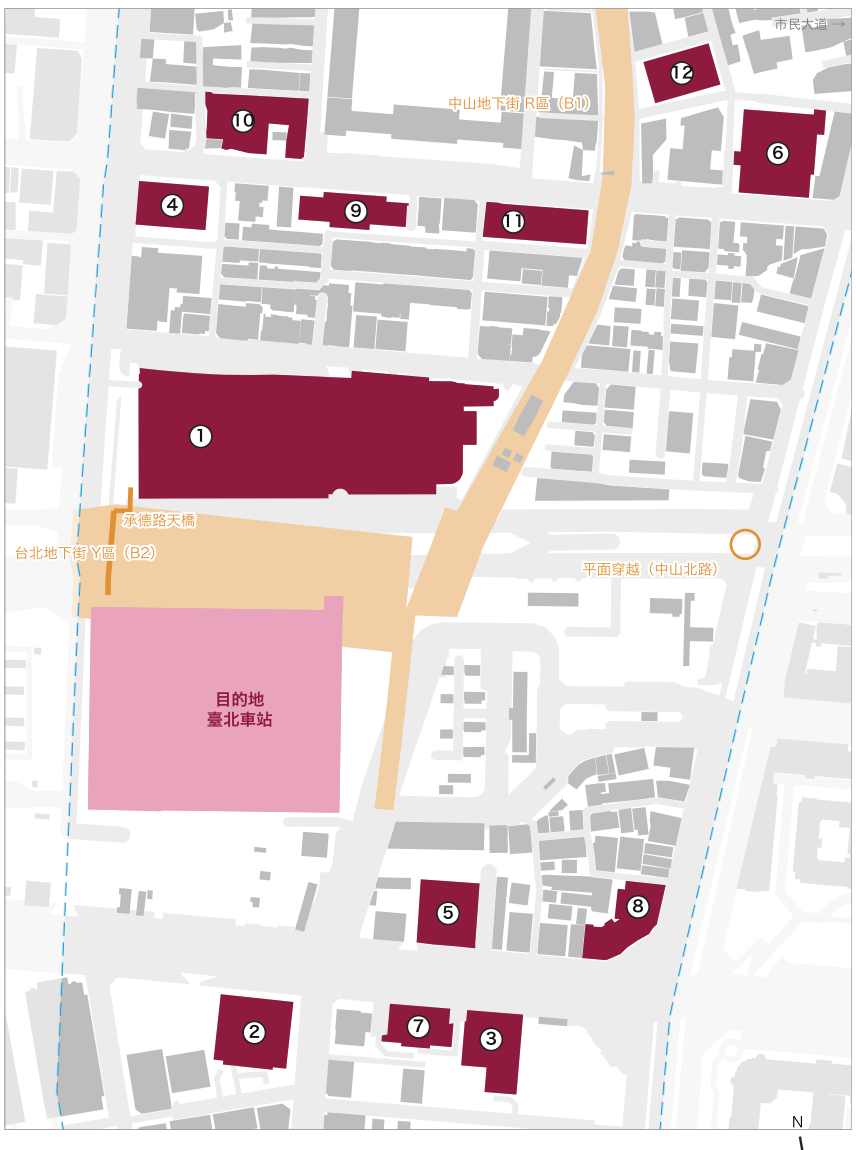

	名稱／量體	人流來源	往車站路徑
1	京站時尚廣場／臺北轉運站　約 27.8 萬㎡・24 層・轉乘＋商業	國道客運轉運站（臺北轉運站，2009 啟用）之轉乘旅客；京站商場購物人潮（店家點：餐飲 31、零售 4 家）；君品酒店住客、威秀影城觀眾	北側，須穿越大道；經 R2 入口 11 m 進中山地下街 R區
2	壽德大樓　約 3.9 萬㎡・20 層・商業	20 層商辦之上班族與洽公民眾（健保署台北業務組、補習班等商辦 9 家）；地面層餐飲 9 家之顧客	南側，不須穿越大道；至捷運 M6 出口 3 m
3	崇聖大樓　約 3.3 萬㎡・23 層・商業	19 - 23 層商辦之上班族（中國信託、東森電視等）	南側，不須穿越大道；至捷運 M7 出口 36 m
4	Jingwang（集合住宅）　約 2.7 萬㎡・32 層・住宅	32 層集合住宅（2022 完工，高 122 m）之住戶通勤、通學	北側，須穿越大道；經 Y9 入口 211 m 進台北地下街 Y區
5	天成大飯店　約 2.5 萬㎡・17 層・旅館	17 層旅館之住客（站前旅館，住宿與車站轉乘）；餐廳 5 家之顧客	南側，不須穿越大道；至捷運 M7 出口 22 m
6	中山辦公大樓　約 2.3 萬㎡・11 層・辦公	市府辦公大樓（OSM office=government）之公務員與洽公民眾（市立圖書館長安分館、自來水北區營業處等）	北側，須穿越大道；經 R4 入口 104 m 進中山地下街 R區
7	中央保險大樓　約 2.0 萬㎡・20 層・商業	20 層商辦之上班族（滙豐銀行等）	南側，不須穿越大道；至捷運 M8 出口 29 m
8	中央大樓　約 1.6 萬㎡・11 層・商業	11 層商業大樓之上班族與顧客（店家 10 家：餐飲、零售、運動用品）	南側，不須穿越大道；至捷運 M7 出口 45 m
9	第五大道　約 1.5 萬㎡・15 層・商業	12 - 15 層住商大樓之住戶與上班族（台北富邦銀行）	北側，須穿越大道；經 R3 入口 103 m 進中山地下街 R區
10	住宅（OSM 未具名）　約 1.4 萬㎡・12 層・住宅	住宅為主、一樓銀行與店家（永豐銀行、7-Eleven）之住戶通勤與顧客	北側，須穿越大道；經 R5 入口 162 m 進中山地下街 R區
11	實益大樓／長安富裕大樓　約 1.3 萬㎡・11 層・店面＋住宅	11 層店面＋住宅之住戶與顧客（店家 9 家：餐飲、便利商店、建材）	北側，須穿越大道；經 R4 入口 38 m 進中山地下街 R區
12	集合住宅（OSM 未具名）　約 1.1 萬㎡・22 層・店面＋住宅	22 層集合住宅之住戶通勤	北側，須穿越大道；經 R5 入口 50 m 進中山地下街 R區
★	臺北車站　約 14.1 萬㎡・7 層	台鐵、高鐵站房，捷運板南線／淡水信義線、機捷轉乘；站內店家點約 101 處（微風台北車站等）	—
—	B03 心中山線形公園	主角之一：線形公園（非建物）。其下中山地下街 R區為北側人流之地下進站路徑	經 R1 - R6 出入口入 R區，接捷運台北車站北端大廳

源頭建築（編號）　目的地：臺北車站　地下街／站體（B1・B2）　人行天橋

© OpenStreetMap contributors / ODbL｜臺北三維模型（2017）

Z3　中山北路—林森北路｜南北通行元素與特性建築

主角：行政院行二行三公辦都更（U17）｜1:4,200（A3）｜圖例見共用圖例

0　50　100　200　400　m　1:4,200（A3）

N

Z3　中山北路—林森北路｜南北通行元素與特性建築

圖例與說明（配合 A3 圖面，1:4,200）

圖例

+2 高架

市民高架

±0 地面

主角：行二行三公辦都更 U17

目的地：商辦／政府機關

目的地：日常生活店家

建物

可通過路口

道路與人行道

單元界線

單元外

通行元素

項目	說明
平面穿越	4 處：中山北、里程 1686 m 處、天津街、林森北
地下街與站體	無
人行天橋	無
穿越間距	147／170 m
最長無穿越段	170 m

主角與目的地

項目	說明
主角	行二行三公辦都更 U17
目的地：商辦／政府機關	10 棟——C 棟大樓、永新林森大廈、行政院大廈、華銀長安大樓 等
目的地：日常生活店家	23 棟，全在北側——金元寶大樓、國際商業大樓、中山雅築 等

日常生活店家（家數）

共 155 家（北 151、南 4）

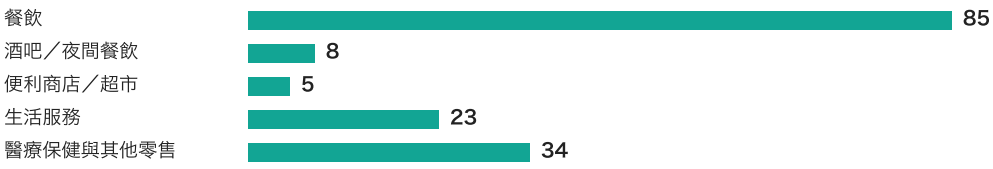

判準：行二行三公辦都更（U17），與其新增人口的目的地——商辦機關（藍）、日常店家（青綠）

資料：臺北三維模型（2017）、OSM、財政部稅籍登記、臺北市正射影像 2025｜© OpenStreetMap contributors

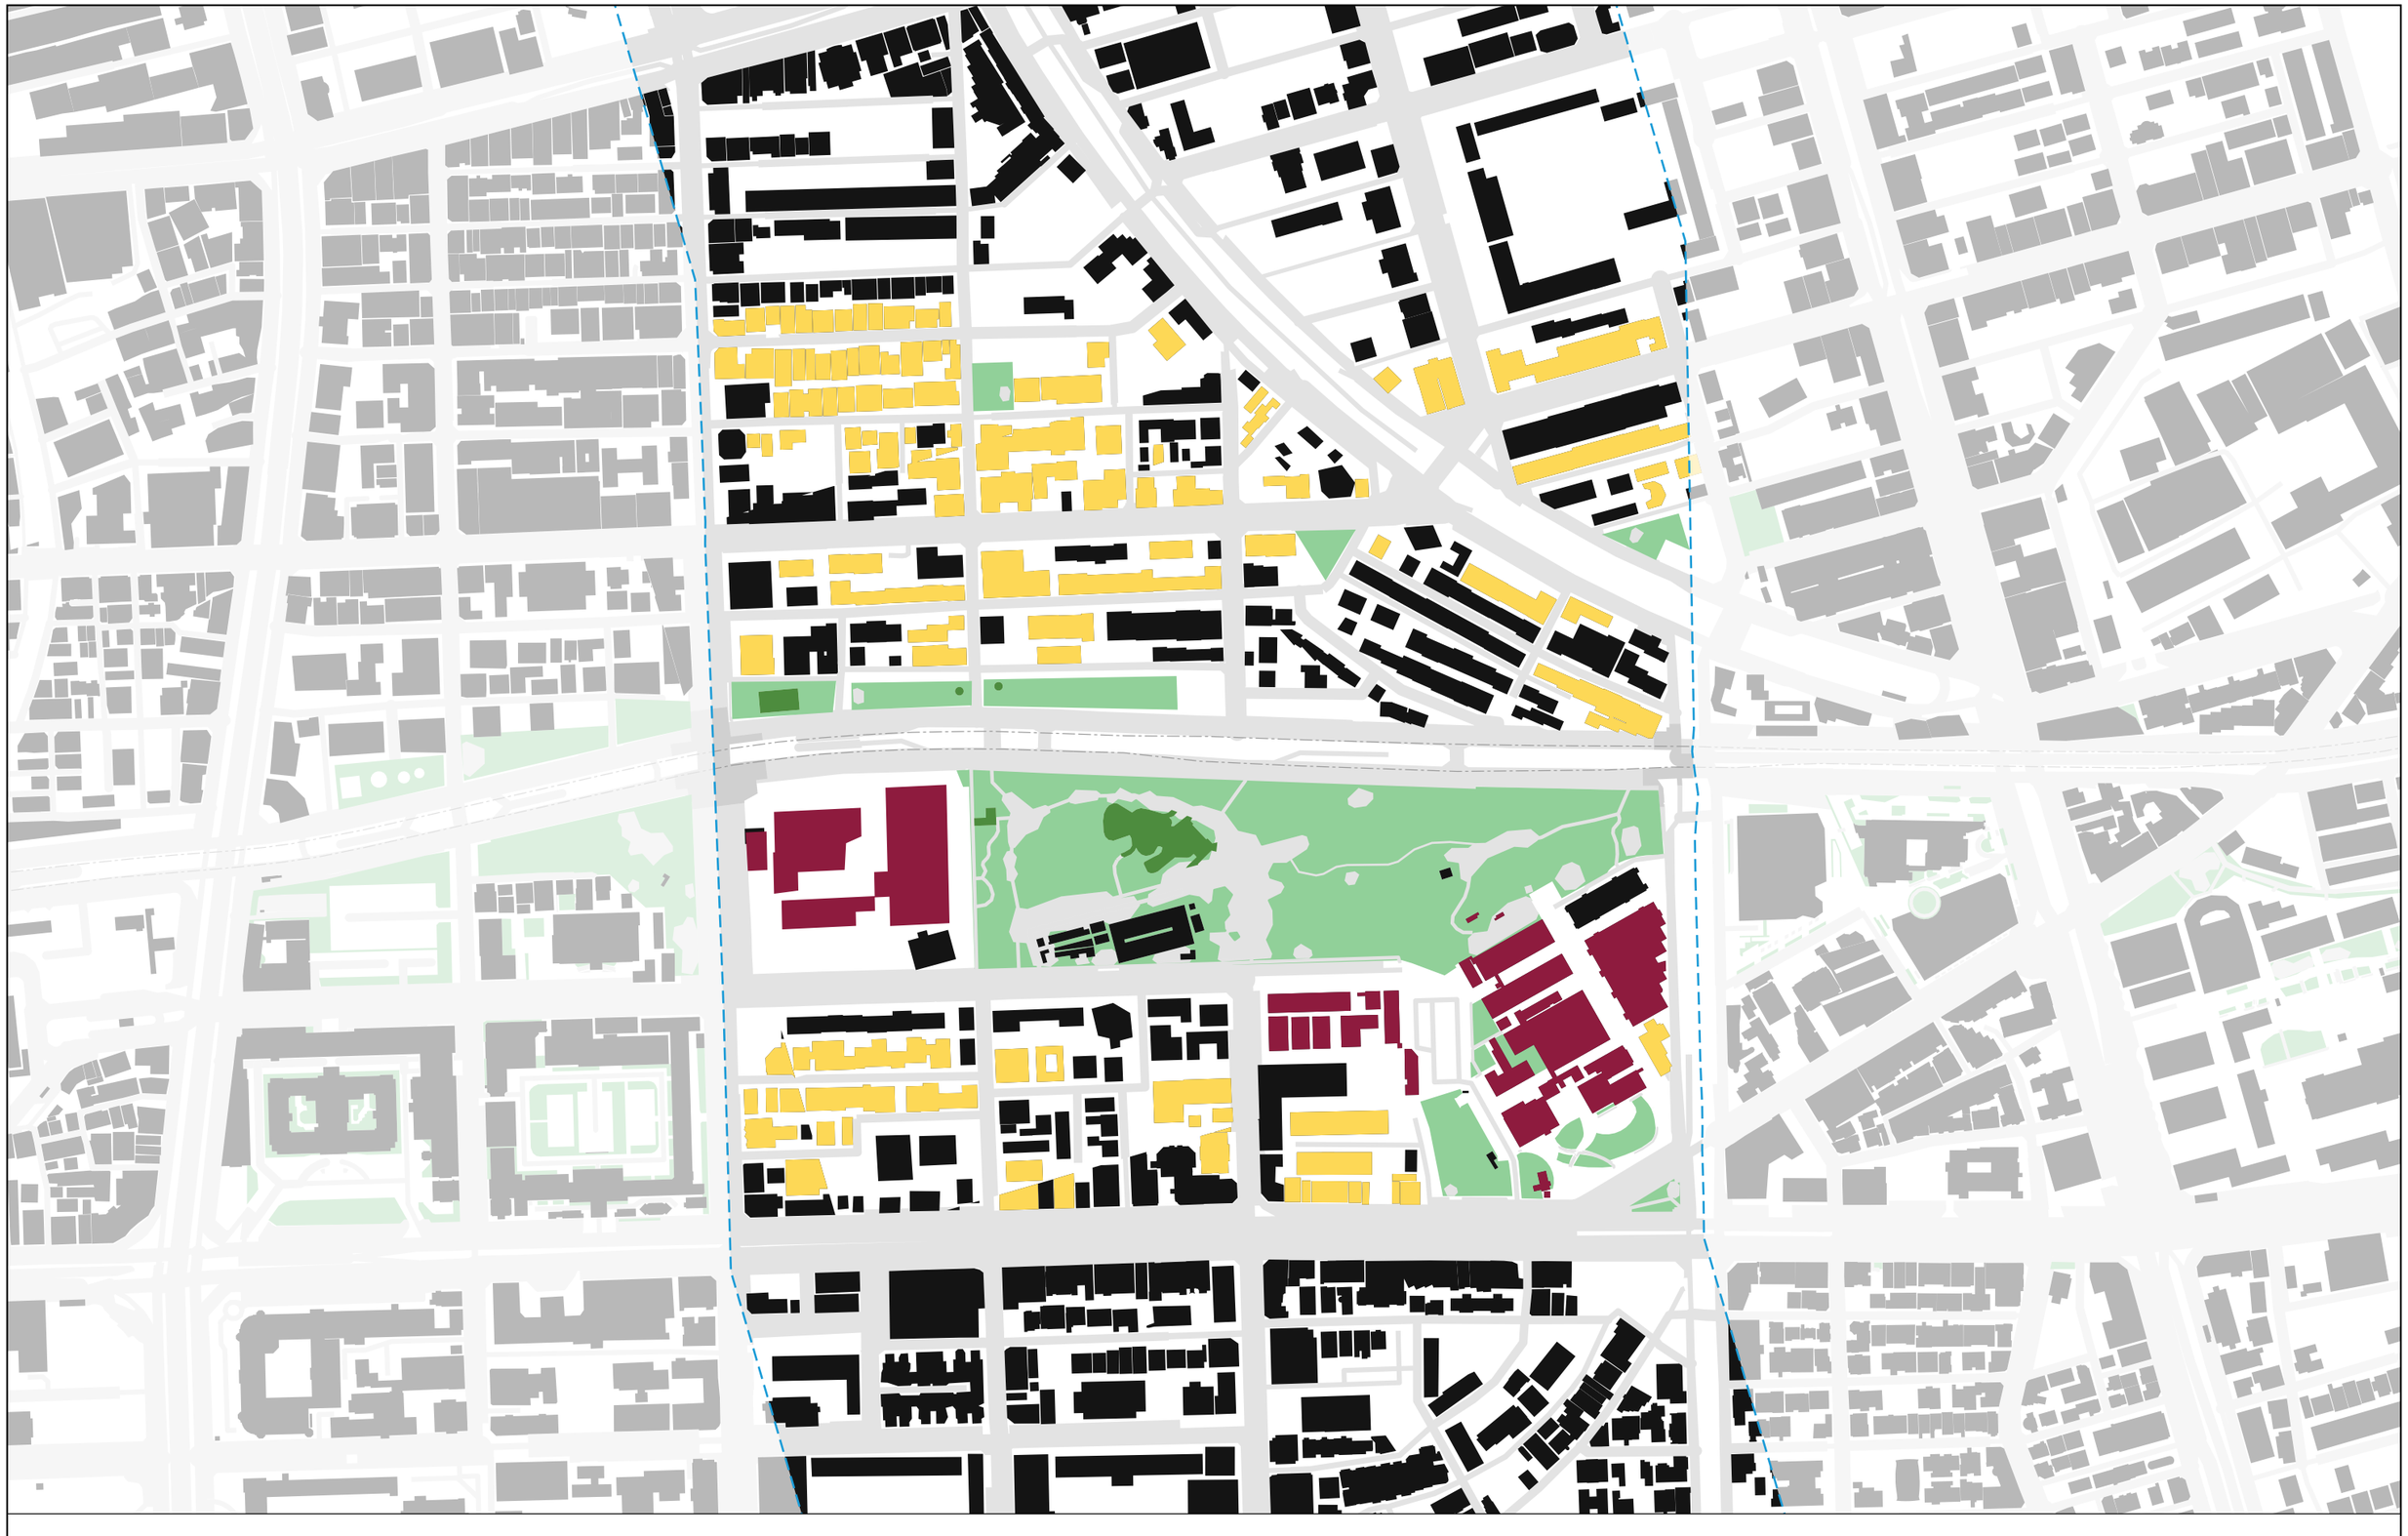

Z4　林森北路—新生高架（金山北路）｜南北通行元素與特性建築

主角：華山（司法園區＋華山1914）｜1:4,200（A3）｜圖例見共用圖例

0　50　100　200　400　m　1:4,200（A3）

N

Z4　林森北路—新生高架（金山北路）｜南北通行元素與特性建築

圖例與說明（配合 A3 圖面，1:4,200）

圖例

+2 高架

市民高架

±0 地面

主角：B01 華山司法園區＋華山 1914

住宅建物

運動場：兒童遊戲場、籃球、體健設施

建物

公園步道與鋪面

純綠地

可通過路口

道路與人行道

單元界線

單元外

通行元素

項目	說明
平面穿越	3 處：林森北、里程 2158 m 處、金山北
地下街與站體	無
人行天橋	無
最長無穿越段	648 m

主角、住宅與運動場

項目	說明
主角	B01 華山司法園區（規劃中）、華山 1914
住宅	約 4,184 戶・7,993 人（北 3,429／南 755 戶）｜65 歲以上 27%
運動場	中央藝文公園（遊戲場 2,102 ㎡、體健 133 ㎡）、華山公園（籃球 421 ㎡）
純綠地	5.14 ha（公園綠地的 72%）｜每戶 12.3 ㎡

判準：華山司法園區＋華山 1914；主軸為運動生活空間——住宅、運動場、綠地

資料：臺北三維模型（2017）、OSM、財政部稅籍登記、臺北市正射影像 2025｜© OpenStreetMap contributors

Z5　新生高架（金山北路）—建國高架｜南北通行元素與特性建築

主角：光華—北科大—建國啤酒廠｜1:4,200（A3）｜圖例見共用圖例

0　50　100　200　400　m　1:4,200（A3）

N

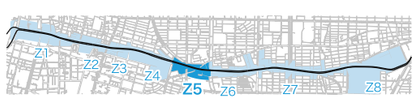

Z5　新生高架（金山北路）—建國高架｜南北通行元素與特性建築

圖例與說明（配合 A3 圖面，1:4,200）

圖例

+2 高架

市民高架

+1 天橋

人行天橋（光華數位新天地—三創空橋）

±0 地面

古蹟：建國啤酒廠

商業空間：大型商場／市場

商業空間：商業大樓／旅館

商業空間：騎樓店面

商業空間：臨街店面

建物

空地：可用空地、步行區、廣場、綠地

可通過路口

道路與人行道

單元界線

單元外

通行元素

項目	說明
平面穿越	4 處：金山北、新生北、八德路二段、建國南
人行天橋	光華數位新天地—三創
穿越間距	204／212／146 m
最長無穿越段	212 m

商業空間、古蹟與空地

項目	說明
大型商場／市場	3 棟・店 185——光華數位新天地、三創、光華玉市
商業大樓／旅館	12 棟・店 34——天成文旅華山町、TOP 松江、長鴻大樓 等
騎樓店面	35 棟・店 189
臨街店面	35 棟・店 100
古蹟	建國啤酒廠（20 棟、22,043 ㎡）
空地	可用空地：平面停車場 3 處、閒置地 1 處
步行區／廣場	三創、光華、希望廣場 等 約 1.4 萬㎡
綠地	約 4,500 ㎡

判準：商業空間之密集——商場、商辦旅館、騎樓店面、臨街店面；紫為建國啤酒廠

資料：臺北三維模型（2017）、OSM、財政部稅籍登記、臺北市正射影像 2025｜© OpenStreetMap contributors

Z6　建國高架—安東街｜南北通行元素與特性建築

主角：長安段公辦都更（U02／U03）｜1:4,200（A3）｜圖例見共用圖例

0　50　100　200　400　m　1:4,200（A3）

N

Z6　建國高架—安東街｜南北通行元素與特性建築

圖例與說明（配合 A3 圖面，1:4,200）

圖例

+2 高架

- 市民高架
- 建國高架

+1 天橋

- 人行天橋（懷生國小西側・OSM 未具名）

±0 地面

- 主角：U02 方案、U03 中崙球場、忠泰美術館街廓、懷生國小、北科大學生宿舍、八德市場
- 主角開放地：空地、校園、瑠公圳公園、U02 法定空地
- 行人穿越道（巷口）
- 建物
- 可通過路口
- 道路與人行道

B1 地下一層

- 忠孝新生站

B2 地下二層

- 忠孝復興站

地下層：大道下方較暗、街廓內較亮

- 單元界線
- 單元外

通行元素

項目	說明
平面穿越	2 處：建國南、安東街
地下街與站體	忠孝新生站（B1）、忠孝復興站（B2）
人行天橋	懷生國小西側
行人穿越道	5 處（巷口）
最長無穿越段	538 m

主角：滲透場所

項目	說明
U02	住都中心公辦都更（23 層住宅＋店鋪）｜北側
忠泰美術館街廓	含明日博、未建築空地｜南側
瑠公圳公園	舊瑠公圳帶狀公園｜南側
懷生國小	北側
北科大學生宿舍	南側
八德市場	北側
U03	現有中崙球場｜北側

判準：滲透場所——公辦都更、美術館街廓、公園、學校、市場

資料：臺北三維模型（2017）、OSM、財政部稅籍登記、臺北市正射影像 2025｜© OpenStreetMap contributors

Z7　安東街—光復南路｜南北通行元素與特性建築

主角：東區北緣宵夜／居酒屋餐飲帶（微風廣場為西端節點）｜1:4,200（A3）｜圖例見共用圖例

0　50　100　200　400　m　1:4,200（A3）

N

Z7　安東街—光復南路｜南北通行元素與特性建築

圖例與說明（配合 A3 圖面，1:4,200）

圖例

+2 高架

- 市民高架

±0 地面

- 夜間餐飲：居酒屋／燒肉串燒
- 夜間餐飲：酒吧／飲酒店
- 夜間餐飲：宵夜小吃
- 夜間餐飲：一般餐飲
- 建物
- 可通過路口
- 道路與人行道

B1 地下一層

- 市民大道地下停車場（建復・復敦・敦延・延吉段）

地下層：大道下方較暗、街廓內較亮

- 單元界線
- 單元外

通行元素

項目	說明
平面穿越	10 處：復興南、大安路、敦化南、延吉街、光復南 及 3 處行人穿越道
地下停車場	市民大道地下停車場（建復、復敦、敦延、延吉段）
人行天橋	無
最長無穿越段	316 m

夜間餐飲（建物棟數｜一樓店家數）

項目	說明
居酒屋／燒肉串燒	33｜45——閻白酒場、武藏居食屋、菜鳥居酒屋 等
酒吧／飲酒店	15｜23——ZEAL、BOX Taipei、Imbibe 等
宵夜小吃	100｜187——馬祖麵店、林東芳牛肉麵 等
一般餐飲	114｜369

夜間餐飲：型態 × 營業時段

一樓餐飲 624 家（北 181／南 443）・建物 262 棟

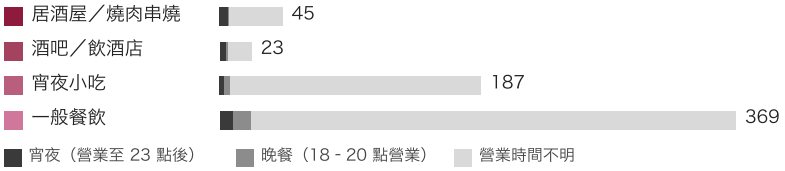

判準：夜間餐飲——居酒屋、酒吧、宵夜小吃、一般餐飲

資料：臺北三維模型（2017）、OSM、財政部稅籍登記、臺北市正射影像 2025｜© OpenStreetMap contributors

Z8　光復南路—基隆路｜南北通行元素與特性建築

主角：松山文創＋大巨蛋＋國家鐵道博物館｜1:4,200（A3）｜圖例見共用圖例

0　50　100　200　400　m　1:4,200（A3）

N

Z8　光復南路—基隆路｜南北通行元素與特性建築

圖例與說明（配合 A3 圖面，1:4,200）

圖例

+2 高架

市民高架

+1 天橋・匝道

匝道：高架段

±0 地面

主角：國家鐵道博物館（臺北機廠）、松山文創園區、臺北大巨蛋

主角戶外空間

行穿線

匝道：落地段

建物

可通過路口

道路與人行道

單元界線

單元外

通行元素

項目	說明
平面穿越	3 處：光復南、里程 5577 m 處、里程 5726 m 處
市民高架匝道	5 條（落地段兩側不可穿越）
行穿線	136 塊（十字路口與巷口）
穿越間距	150／150 m
最長無穿越段	約 612 m（鐵道博物館南緣至基隆路）

主角：南北兩側三園區

項目	說明
國家鐵道博物館	北側｜建物 7.6 萬㎡、戶外 8.4 萬㎡｜正門朝北，開向市民大道五段
松山文創園區	南側｜建物 2.6 萬㎡、戶外 5.4 萬㎡
臺北大巨蛋	南側｜建物 5.4 萬㎡、戶外 3.4 萬㎡

判準：南北兩側三園區——國家鐵道博物館、松山文創、臺北大巨蛋

資料：臺北三維模型（2017）、OSM、財政部稅籍登記、臺北市正射影像 2025｜© OpenStreetMap contributors